

### Punkt

- Adresspoint
- ★ Duct\_Ende
- ▲ Duct\_Joint
- Pop
- Dp
- Manhole

### Linie

- Duct
- Dropduct

### Duct

- Black
- Blau
- Green
- Orange
- Purple

### Polygon


- Dp\_Cluster
- POP\_Cluster

### DATA

- Flurstück
- Backbone

Projekt	Lindelbach
Datum	01.03.2025
Maßstab	1:500
Blatt	LIND_01 20/1
Bearbeiter	Sefa Coskun



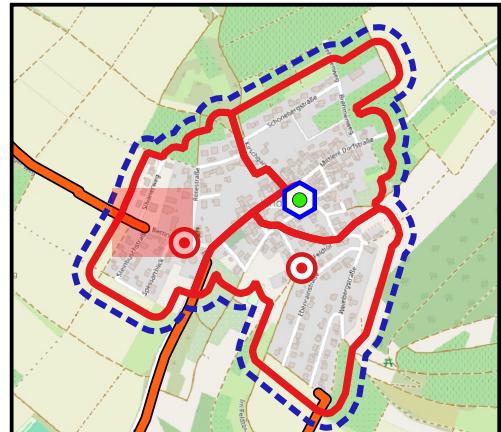

**Punkt**

- Adresspoint
- \* Duct\_Ende
- ▲ Duct\_Joint
- Pop
- Dp
- Manhole

**Linie**

- Dropduct

**Duct**

- Black
- Blau
- Green
- Orange
- Purple

**Polygon**


- Dp\_Cluster
- POP\_Cluster



**DATA**


- Flurstück
- Backbone


Projekt	Lindelbach
Datum	01.03.2025
Maßstab	1:500
Blatt	LIND_01 20/2
Bearbeiter	Sefa Coskun




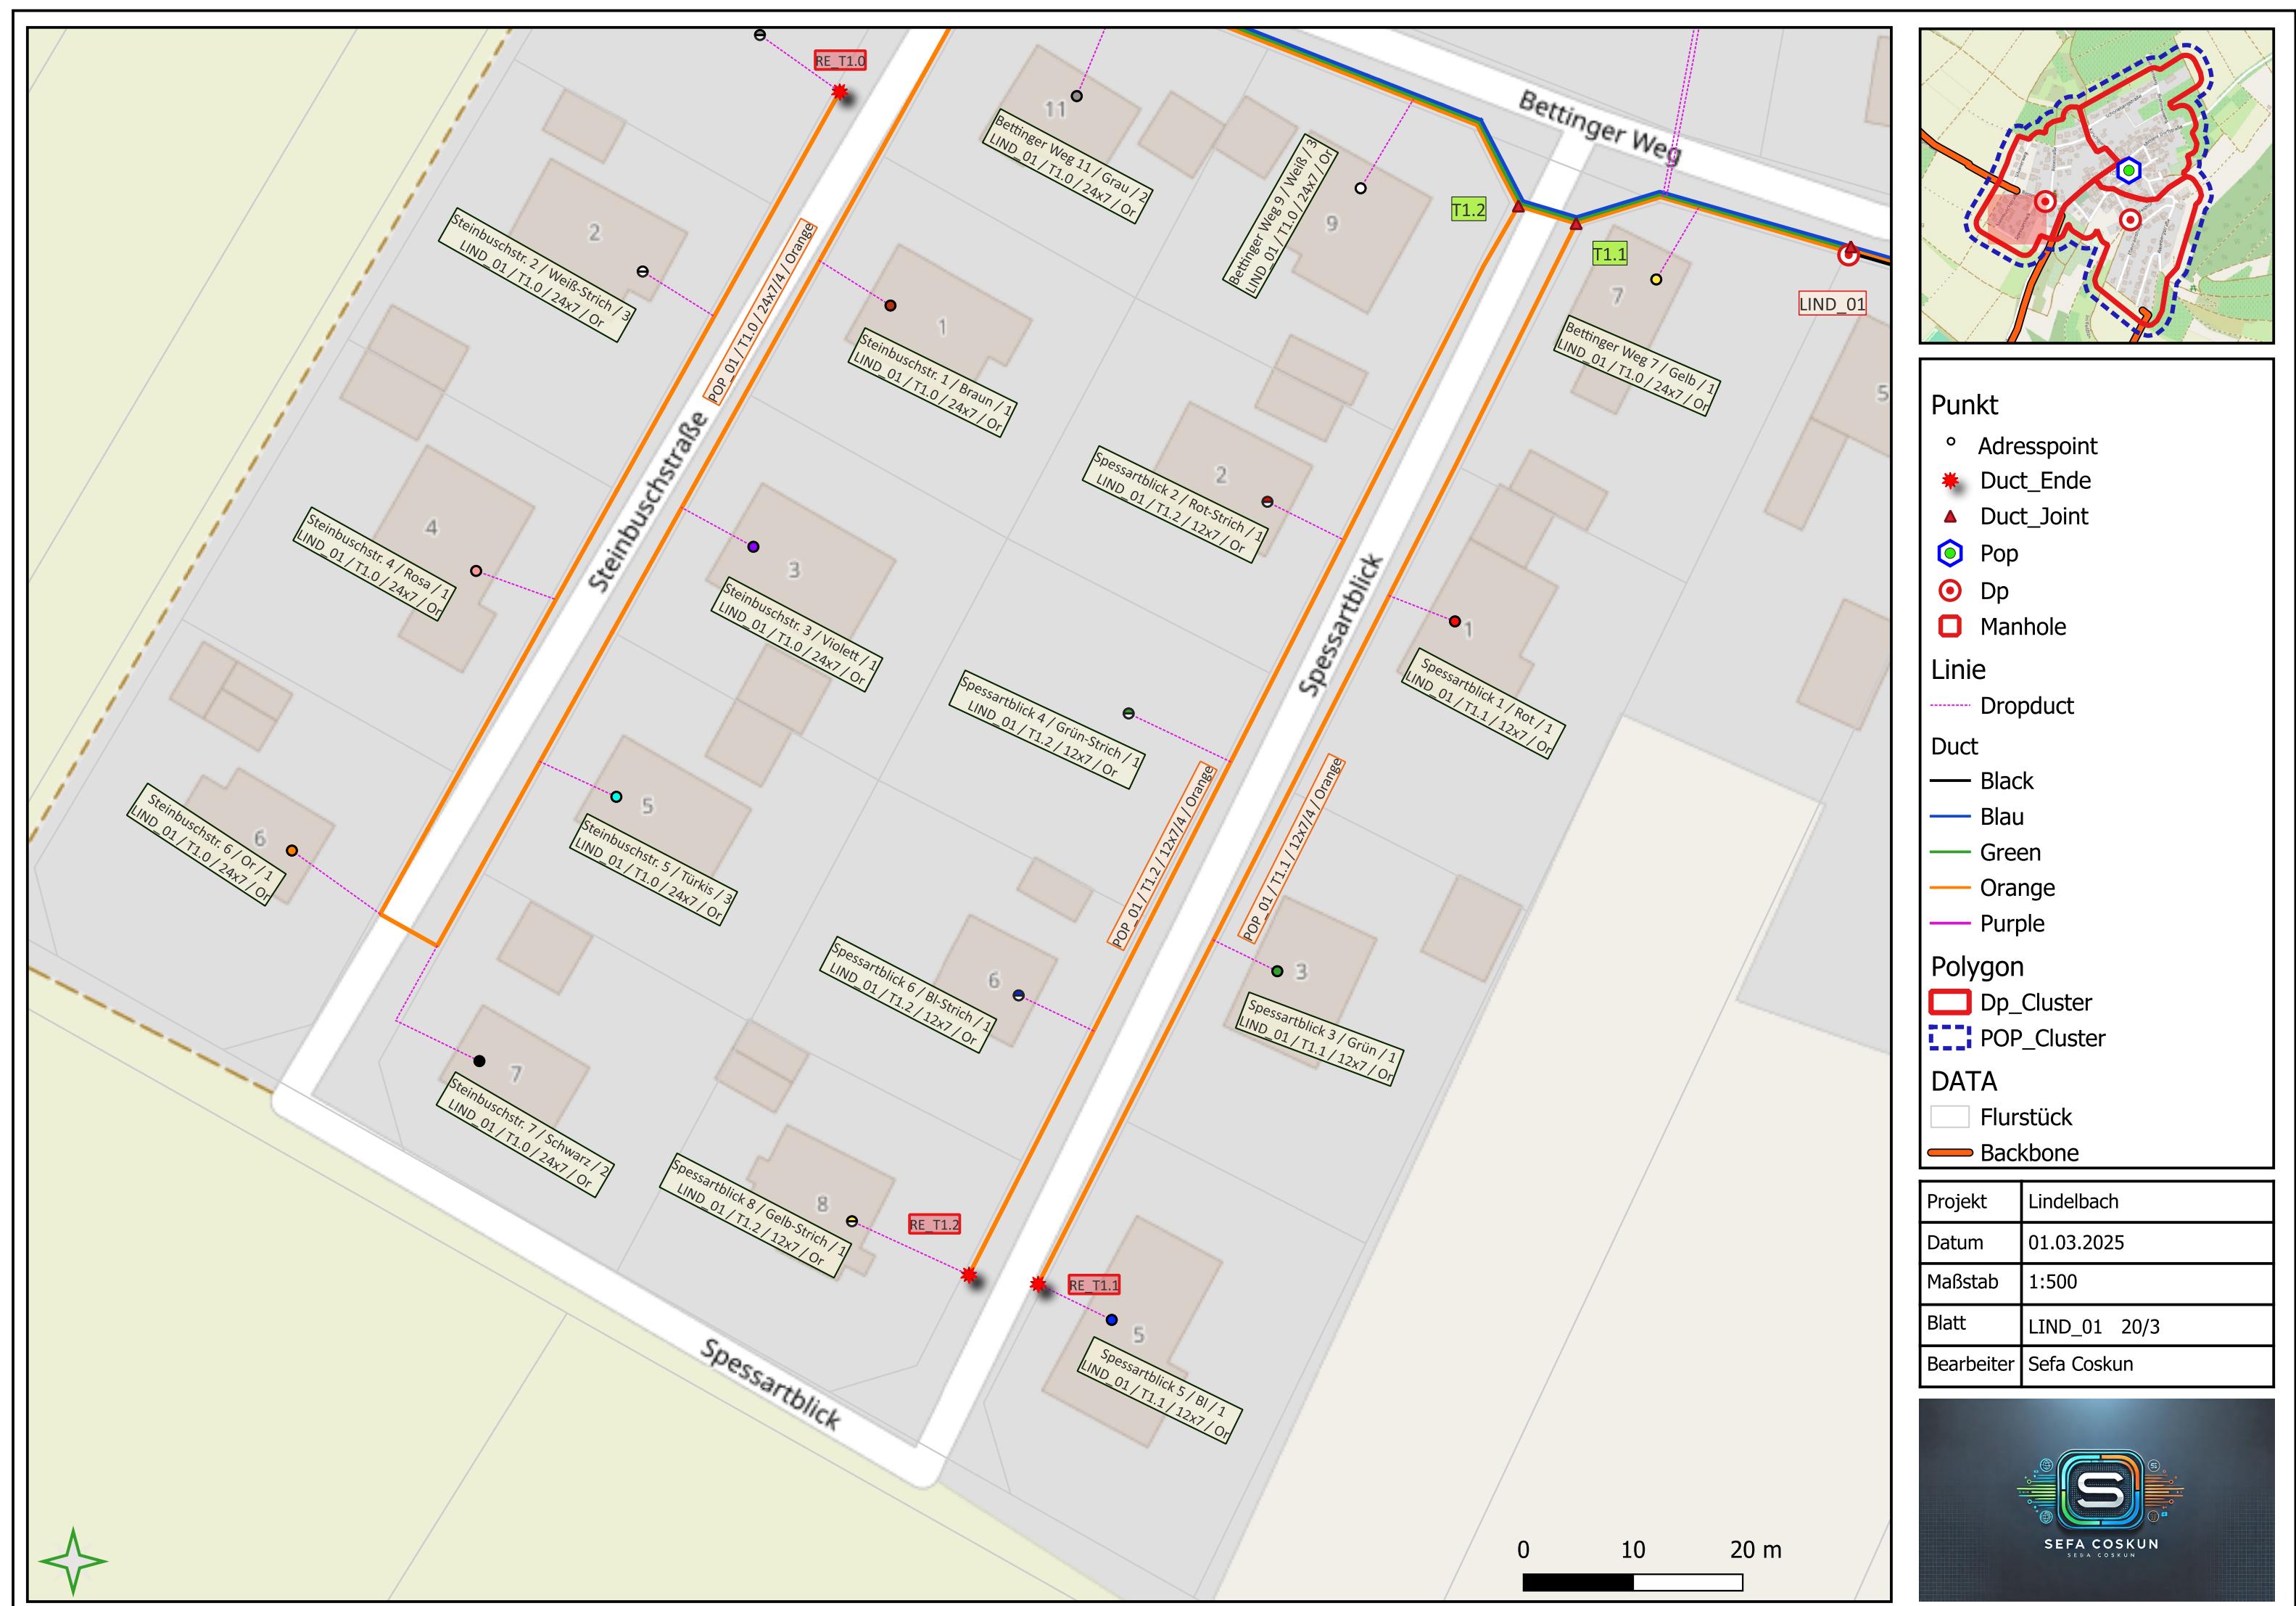

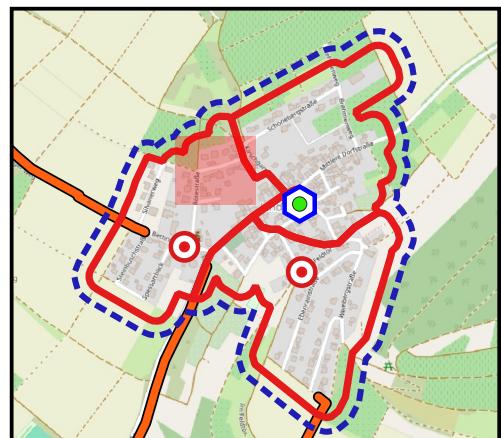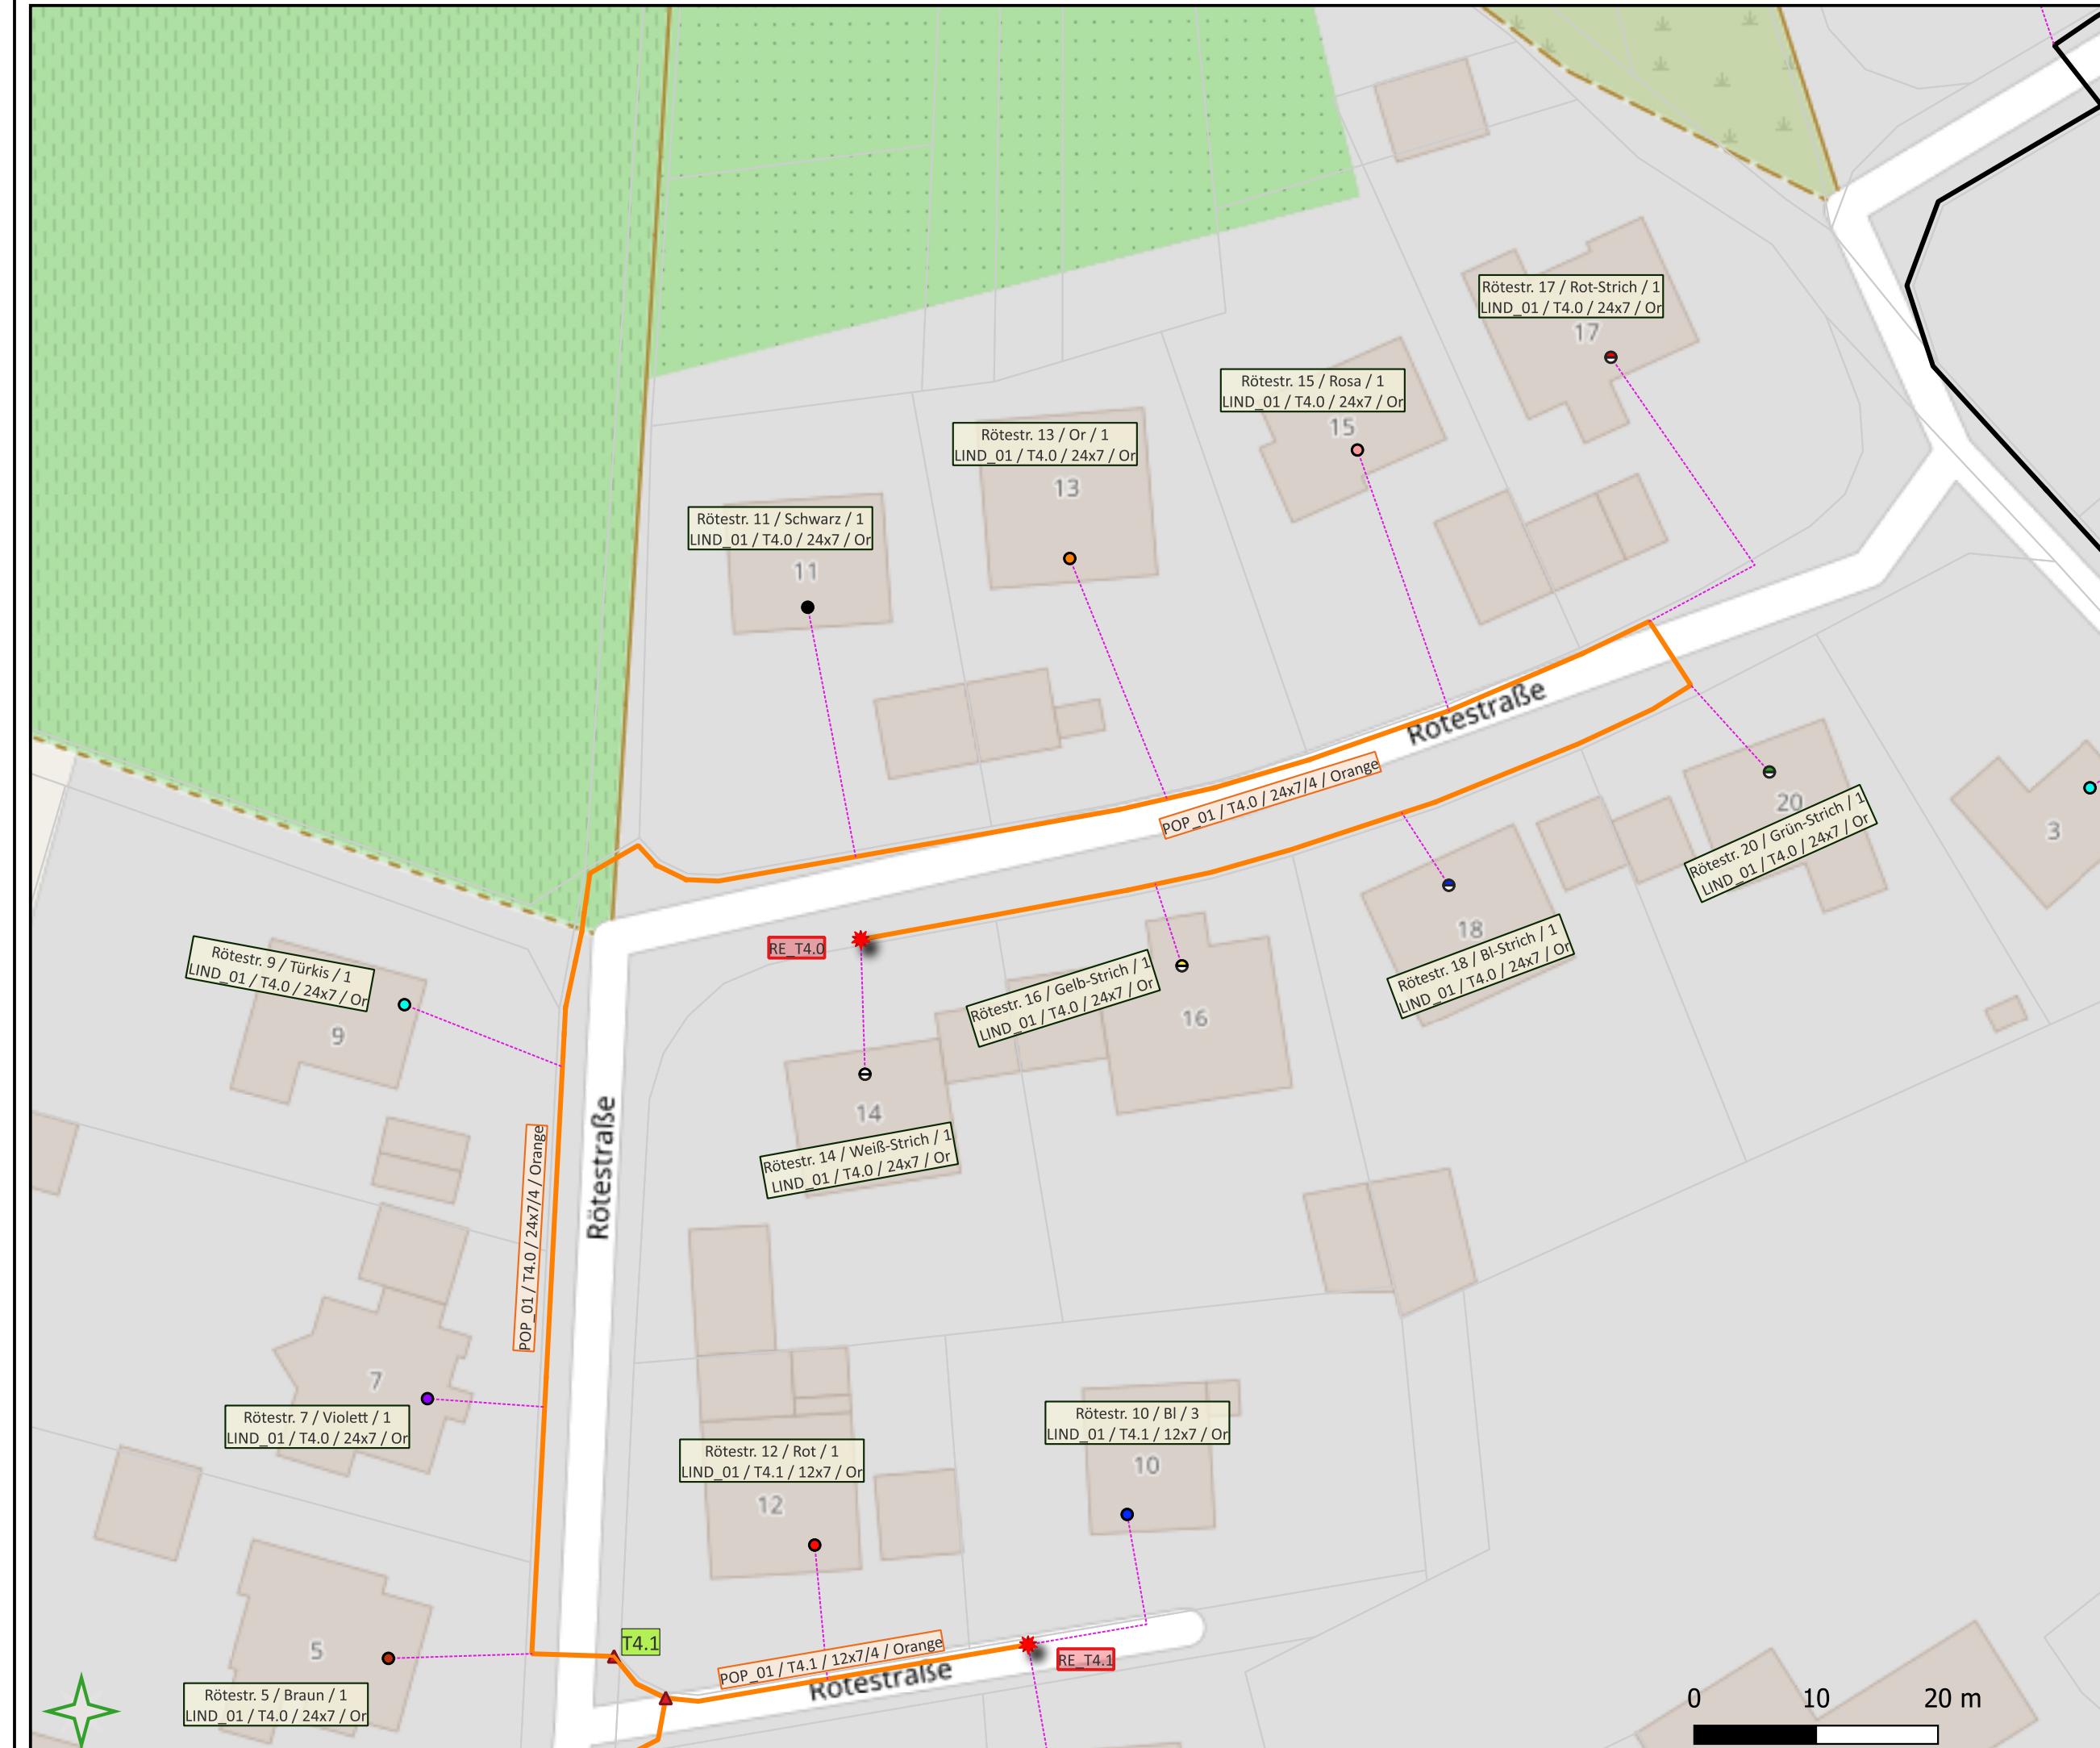

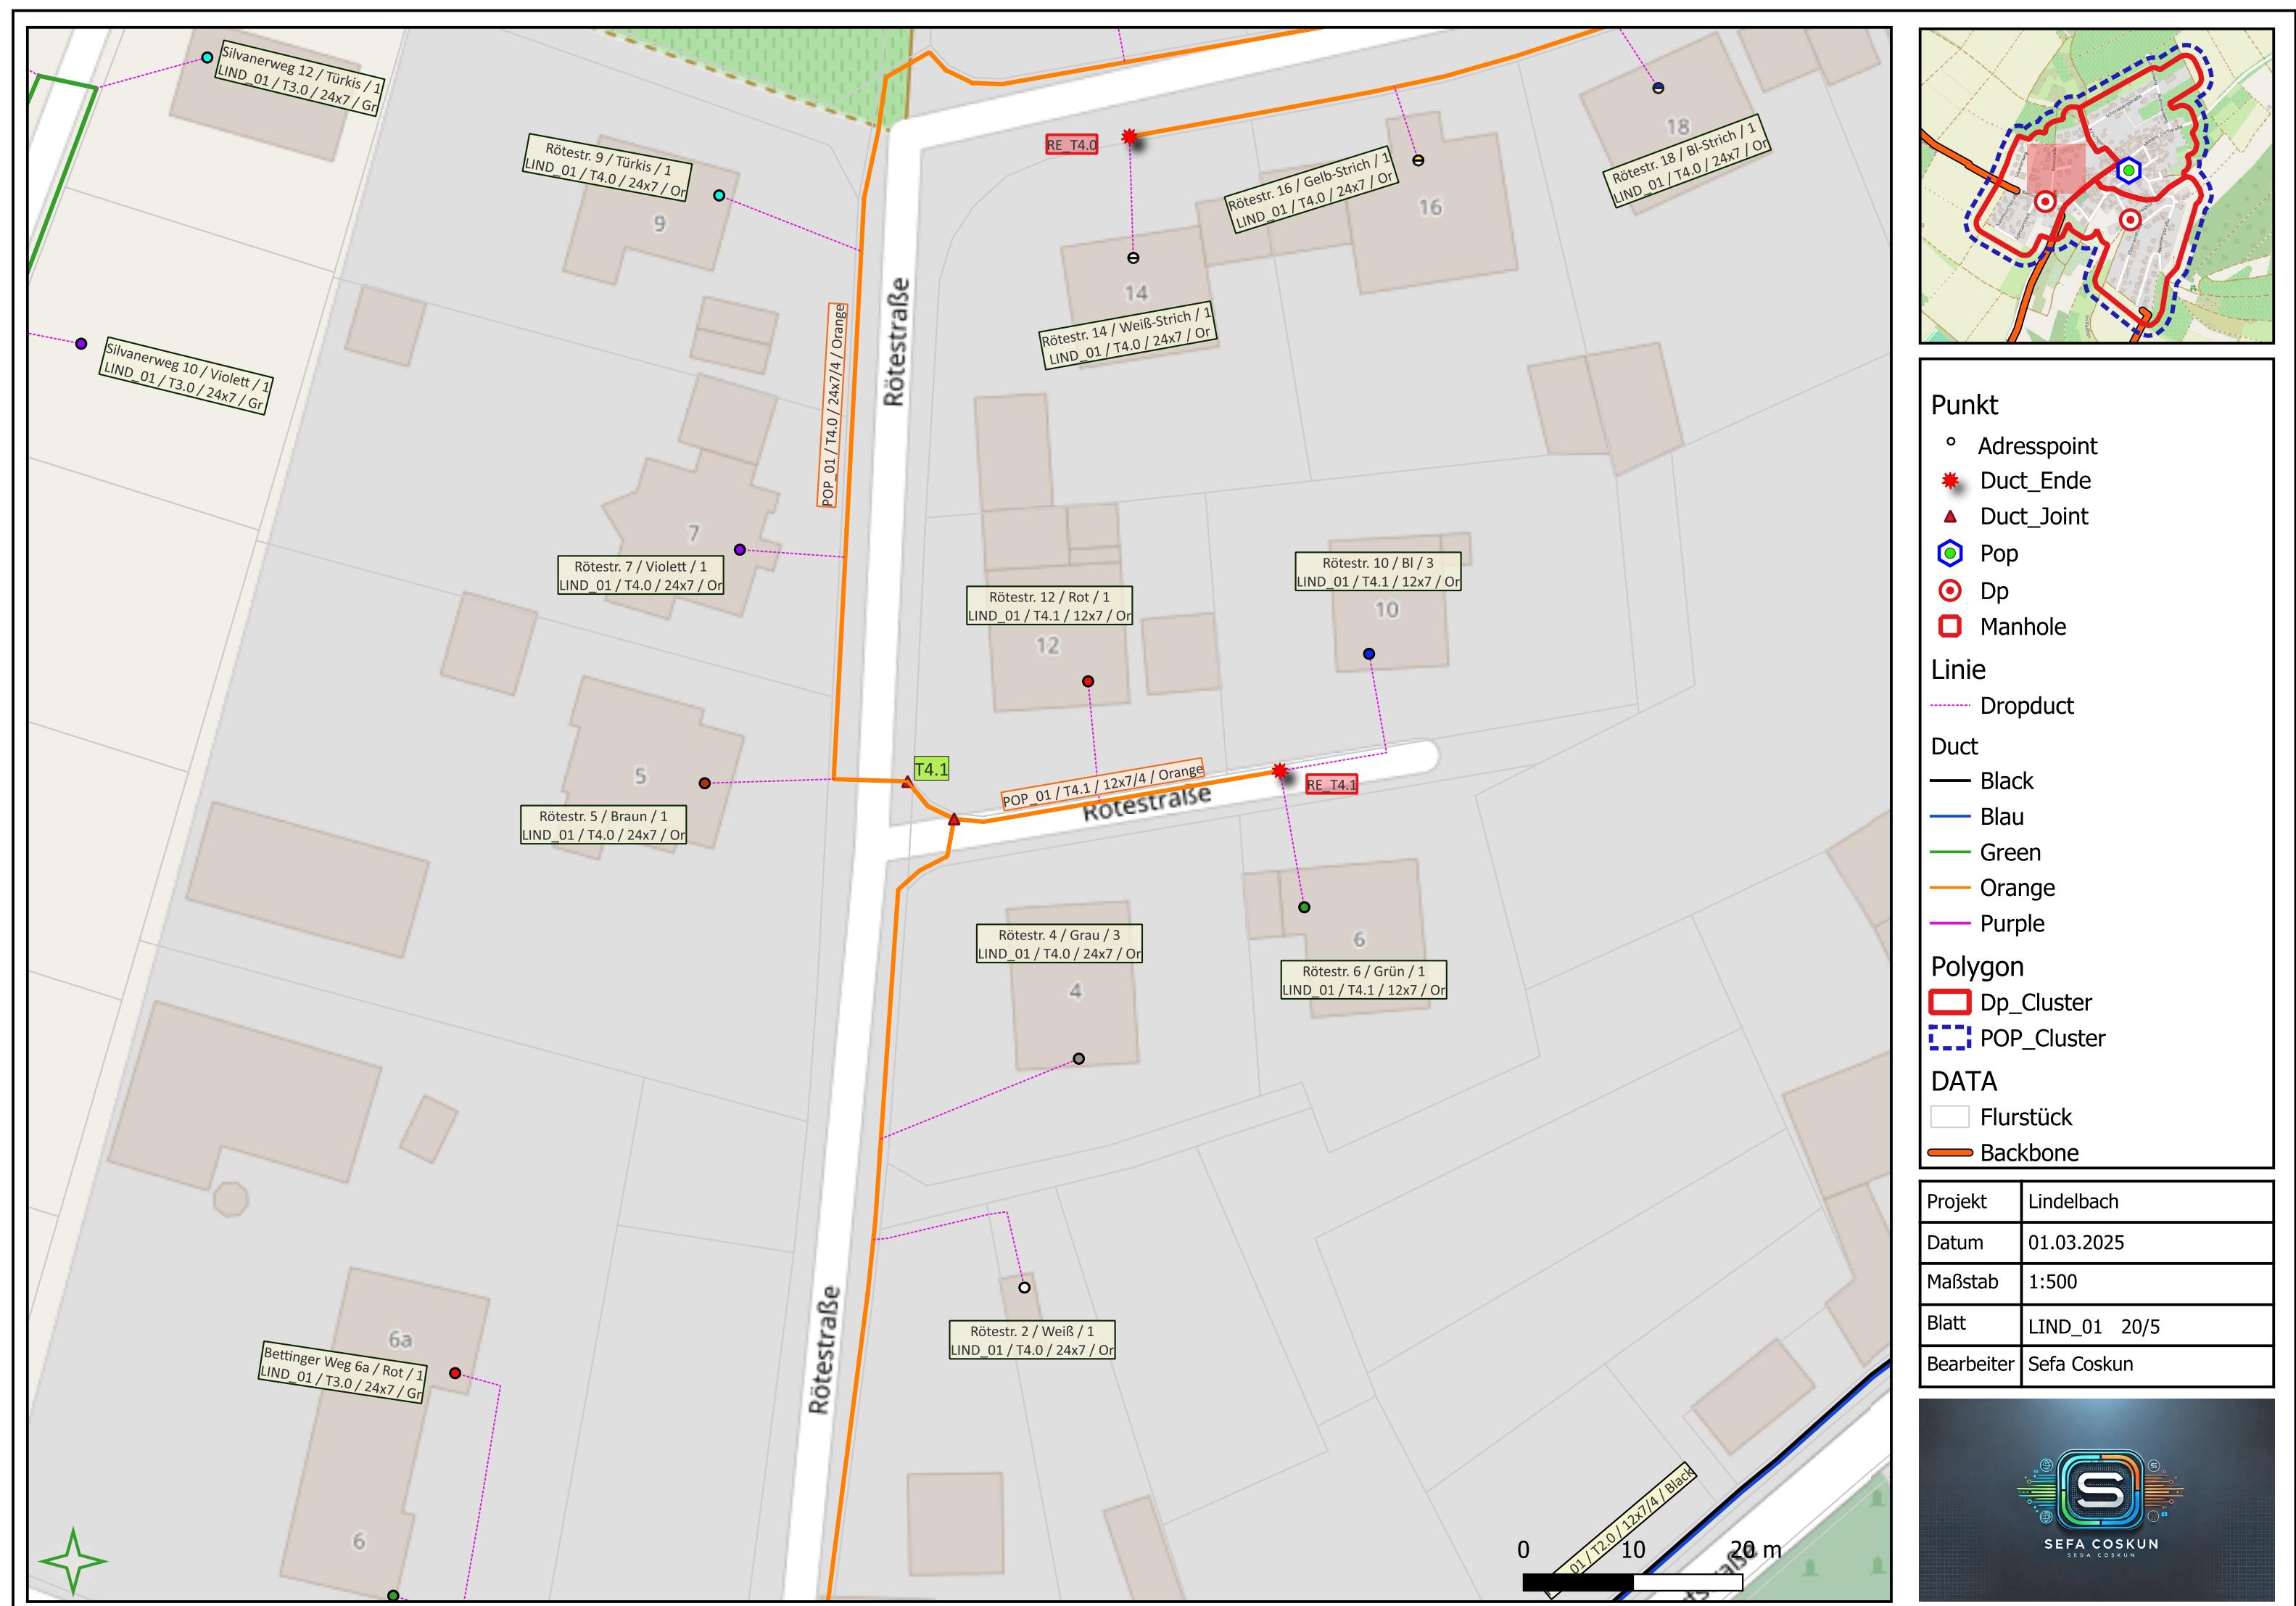

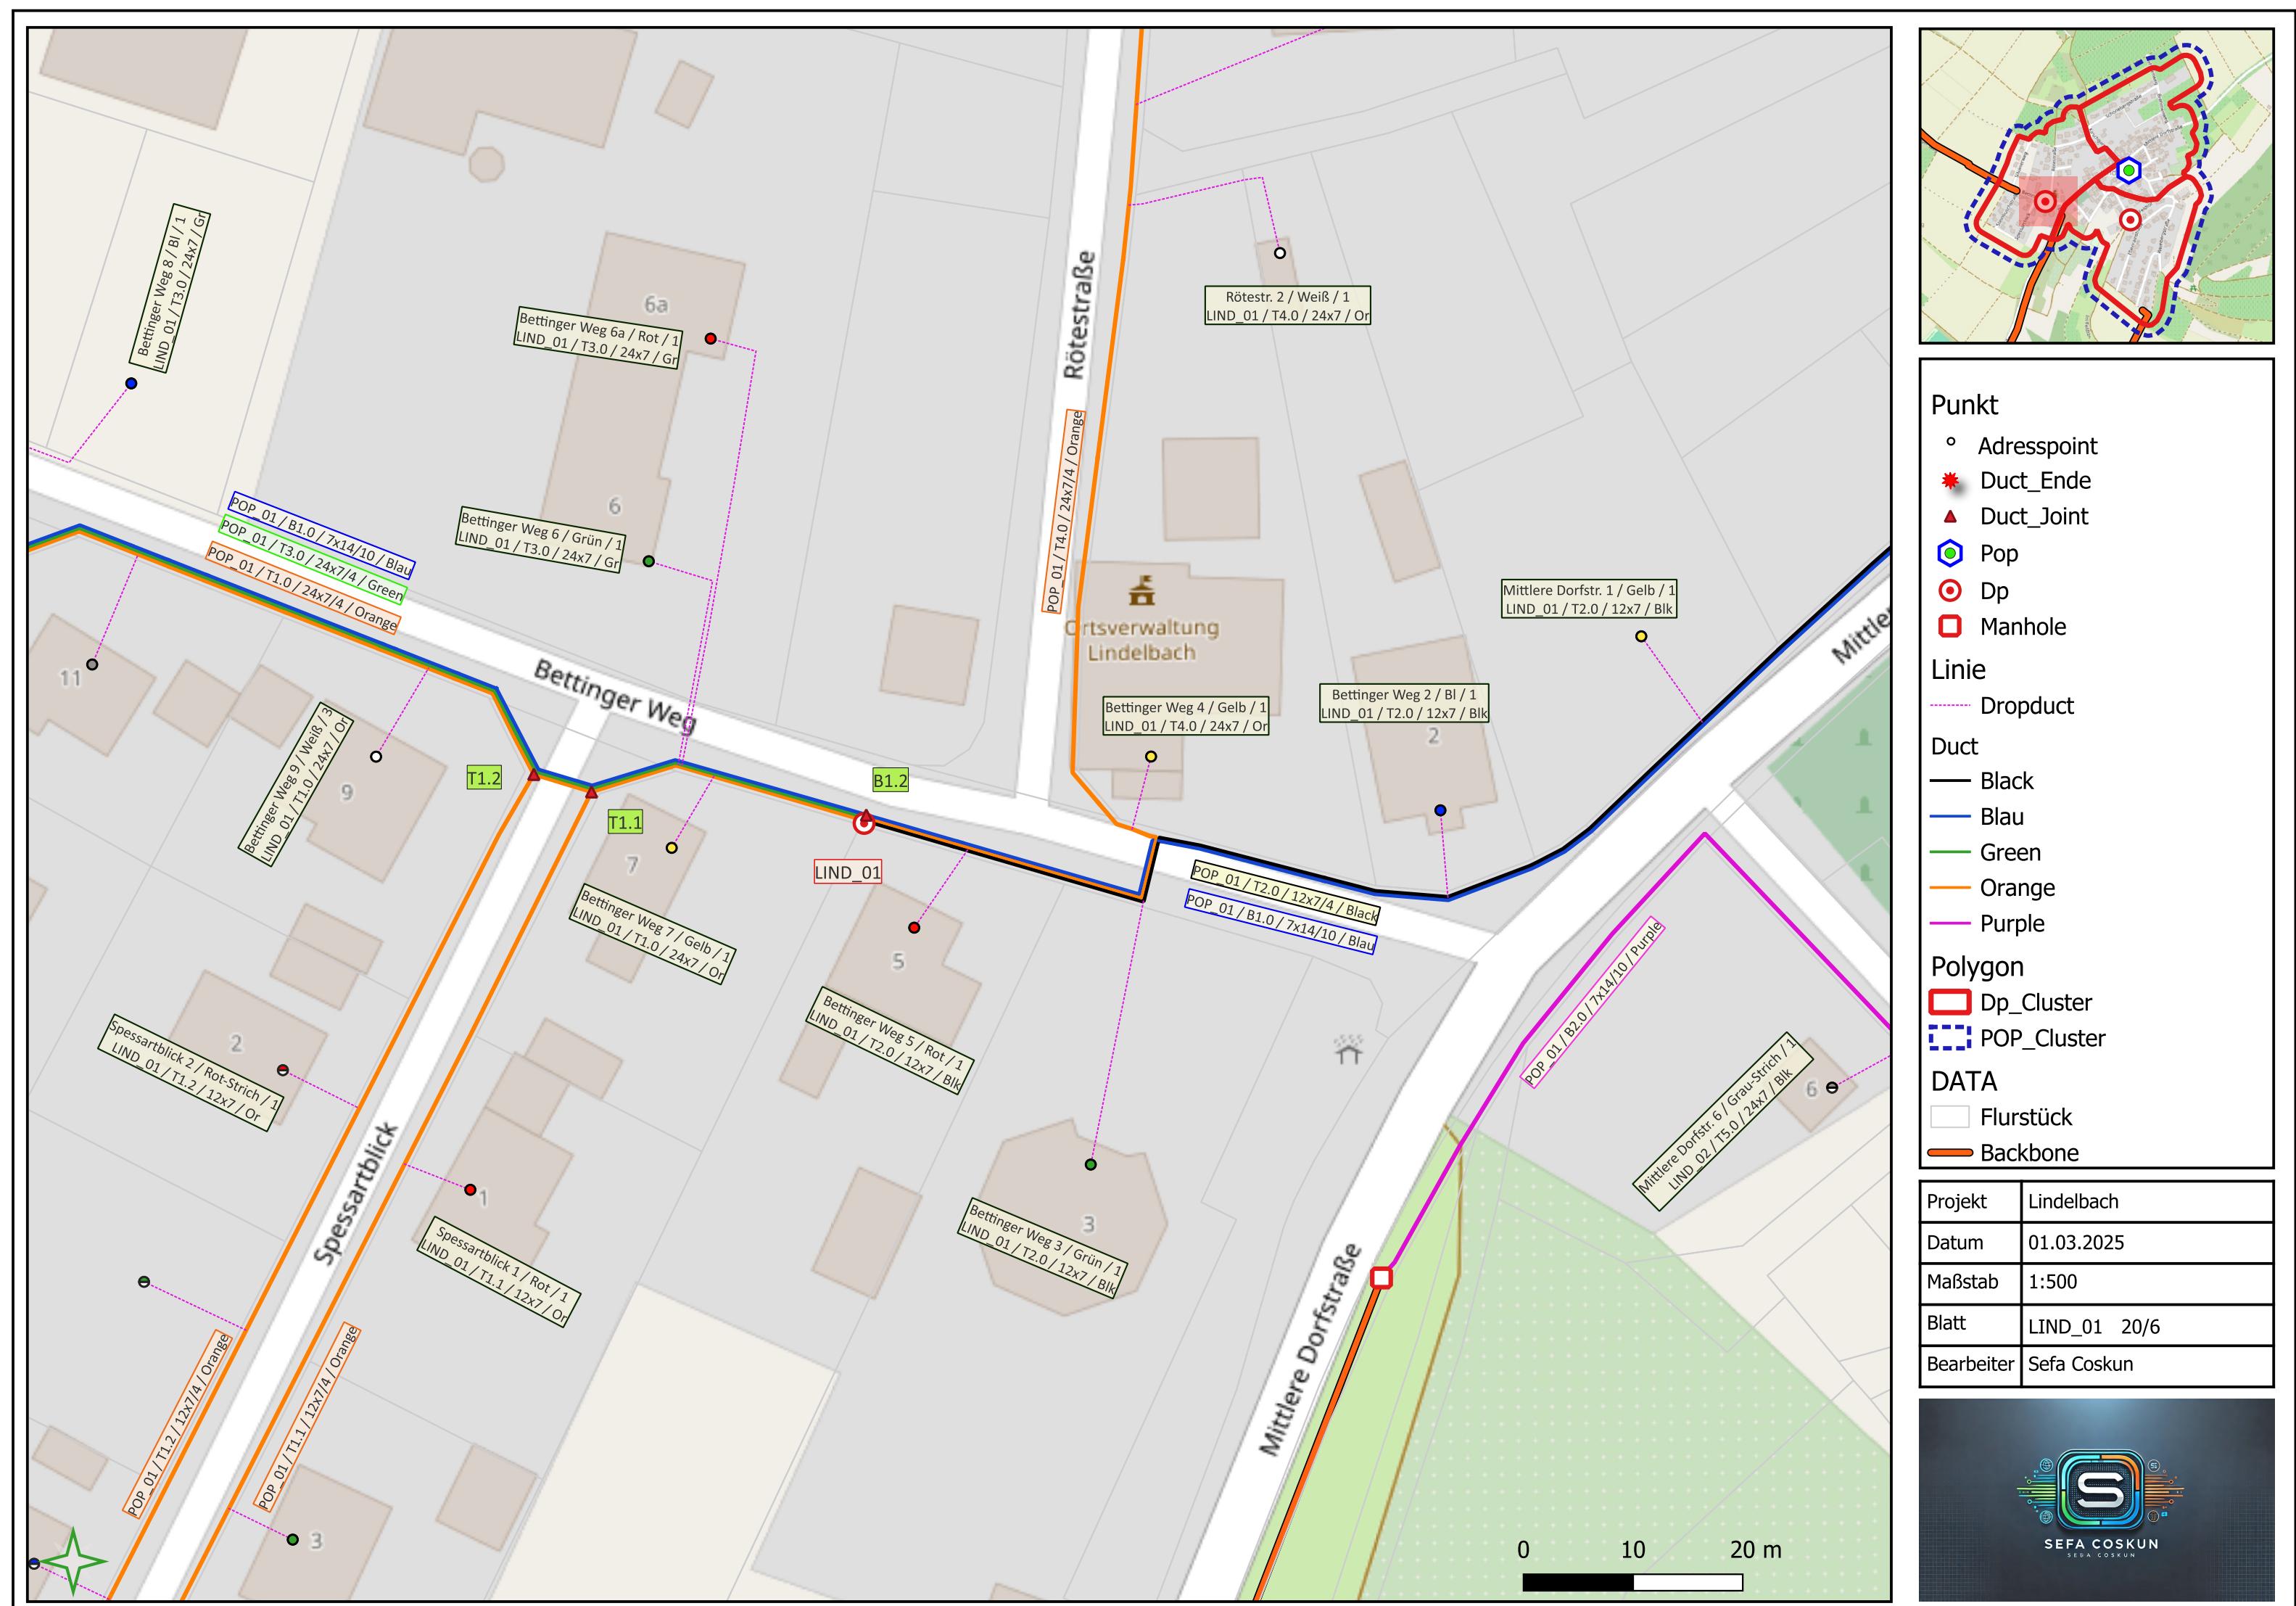

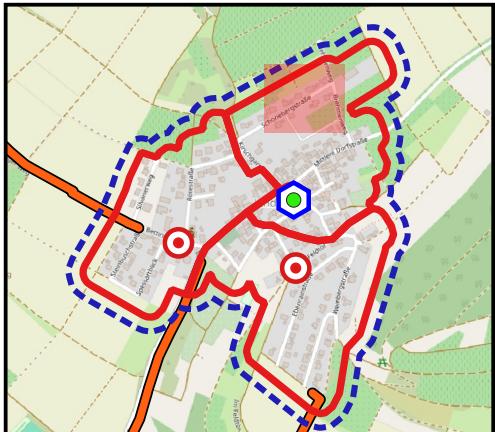

**Punkt**

- Adresspoint
- \* Duct\_Ende
- ▲ Duct\_Joint
- Pop
- Dp
- Manhole

**Linie**

- Dropduct

**Duct**

- Black
- Blue
- Green
- Orange
- Purple

**Polygon**


- Dp\_Cluster
- POP\_Cluster

**DATA**

- Flurstück
- Backbone

Projekt	Lindelbach
Datum	01.03.2025
Maßstab	1:500
Blatt	LIND_03 20/7
Bearbeiter	Sefa Coskun



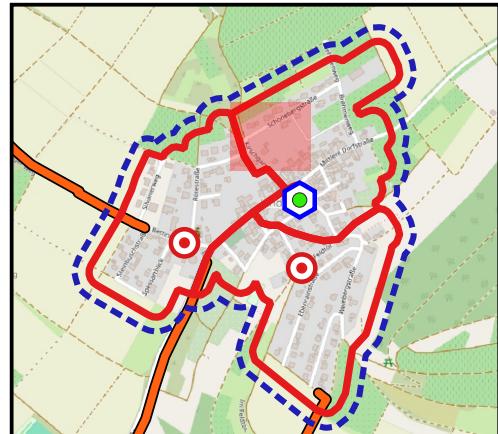

### Punkt

- Adresspoint
- \* Duct\_Ende
- ▲ Duct\_Joint
- Pop
- Dp
- Manhole

### Linie

- Dropduct

### Duct

- Black
- Blue
- Green
- Orange
- Purple

### Polygon


- Dp\_Cluster
- POP\_Cluster



### DATA

- Flurstück
- Backbone

Projekt	Lindelbach
Datum	01.03.2025
Maßstab	1:500
Blatt	LIND_03 20/8
Bearbeiter	Sefa Coskun



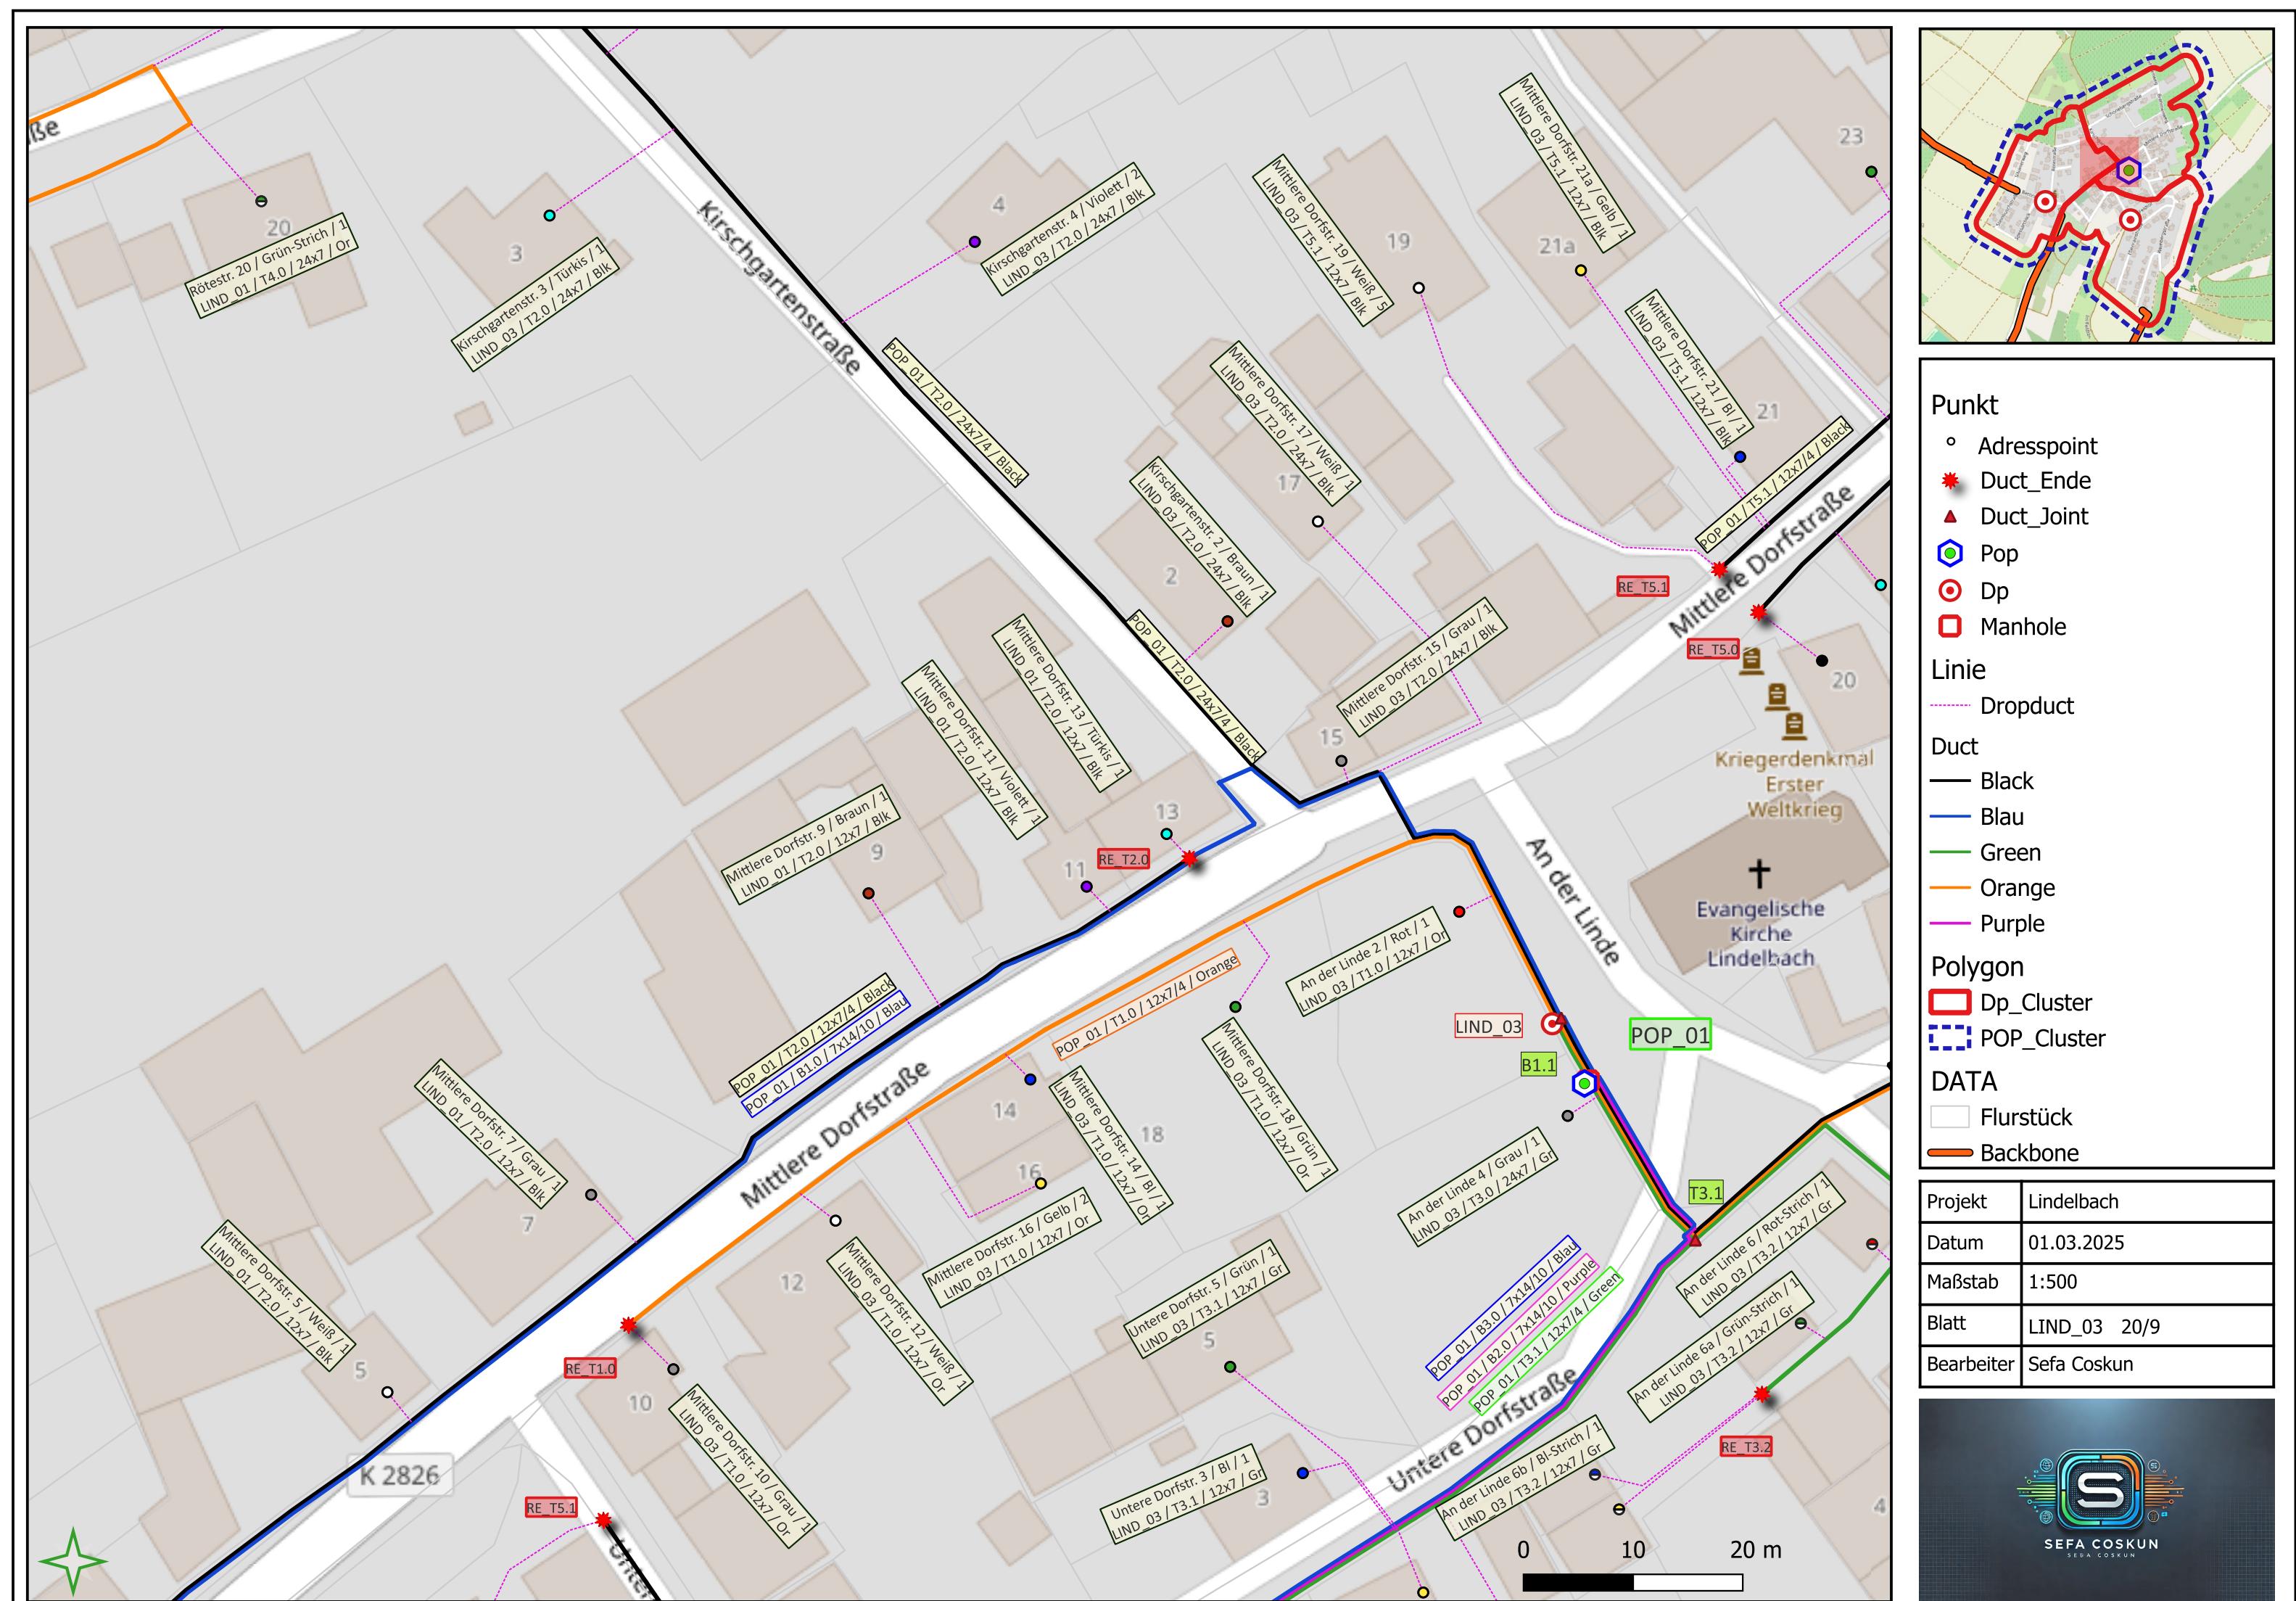

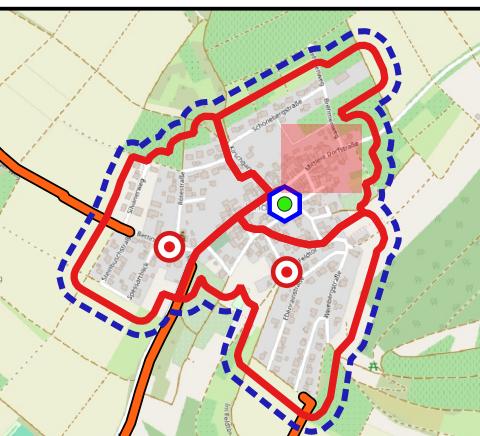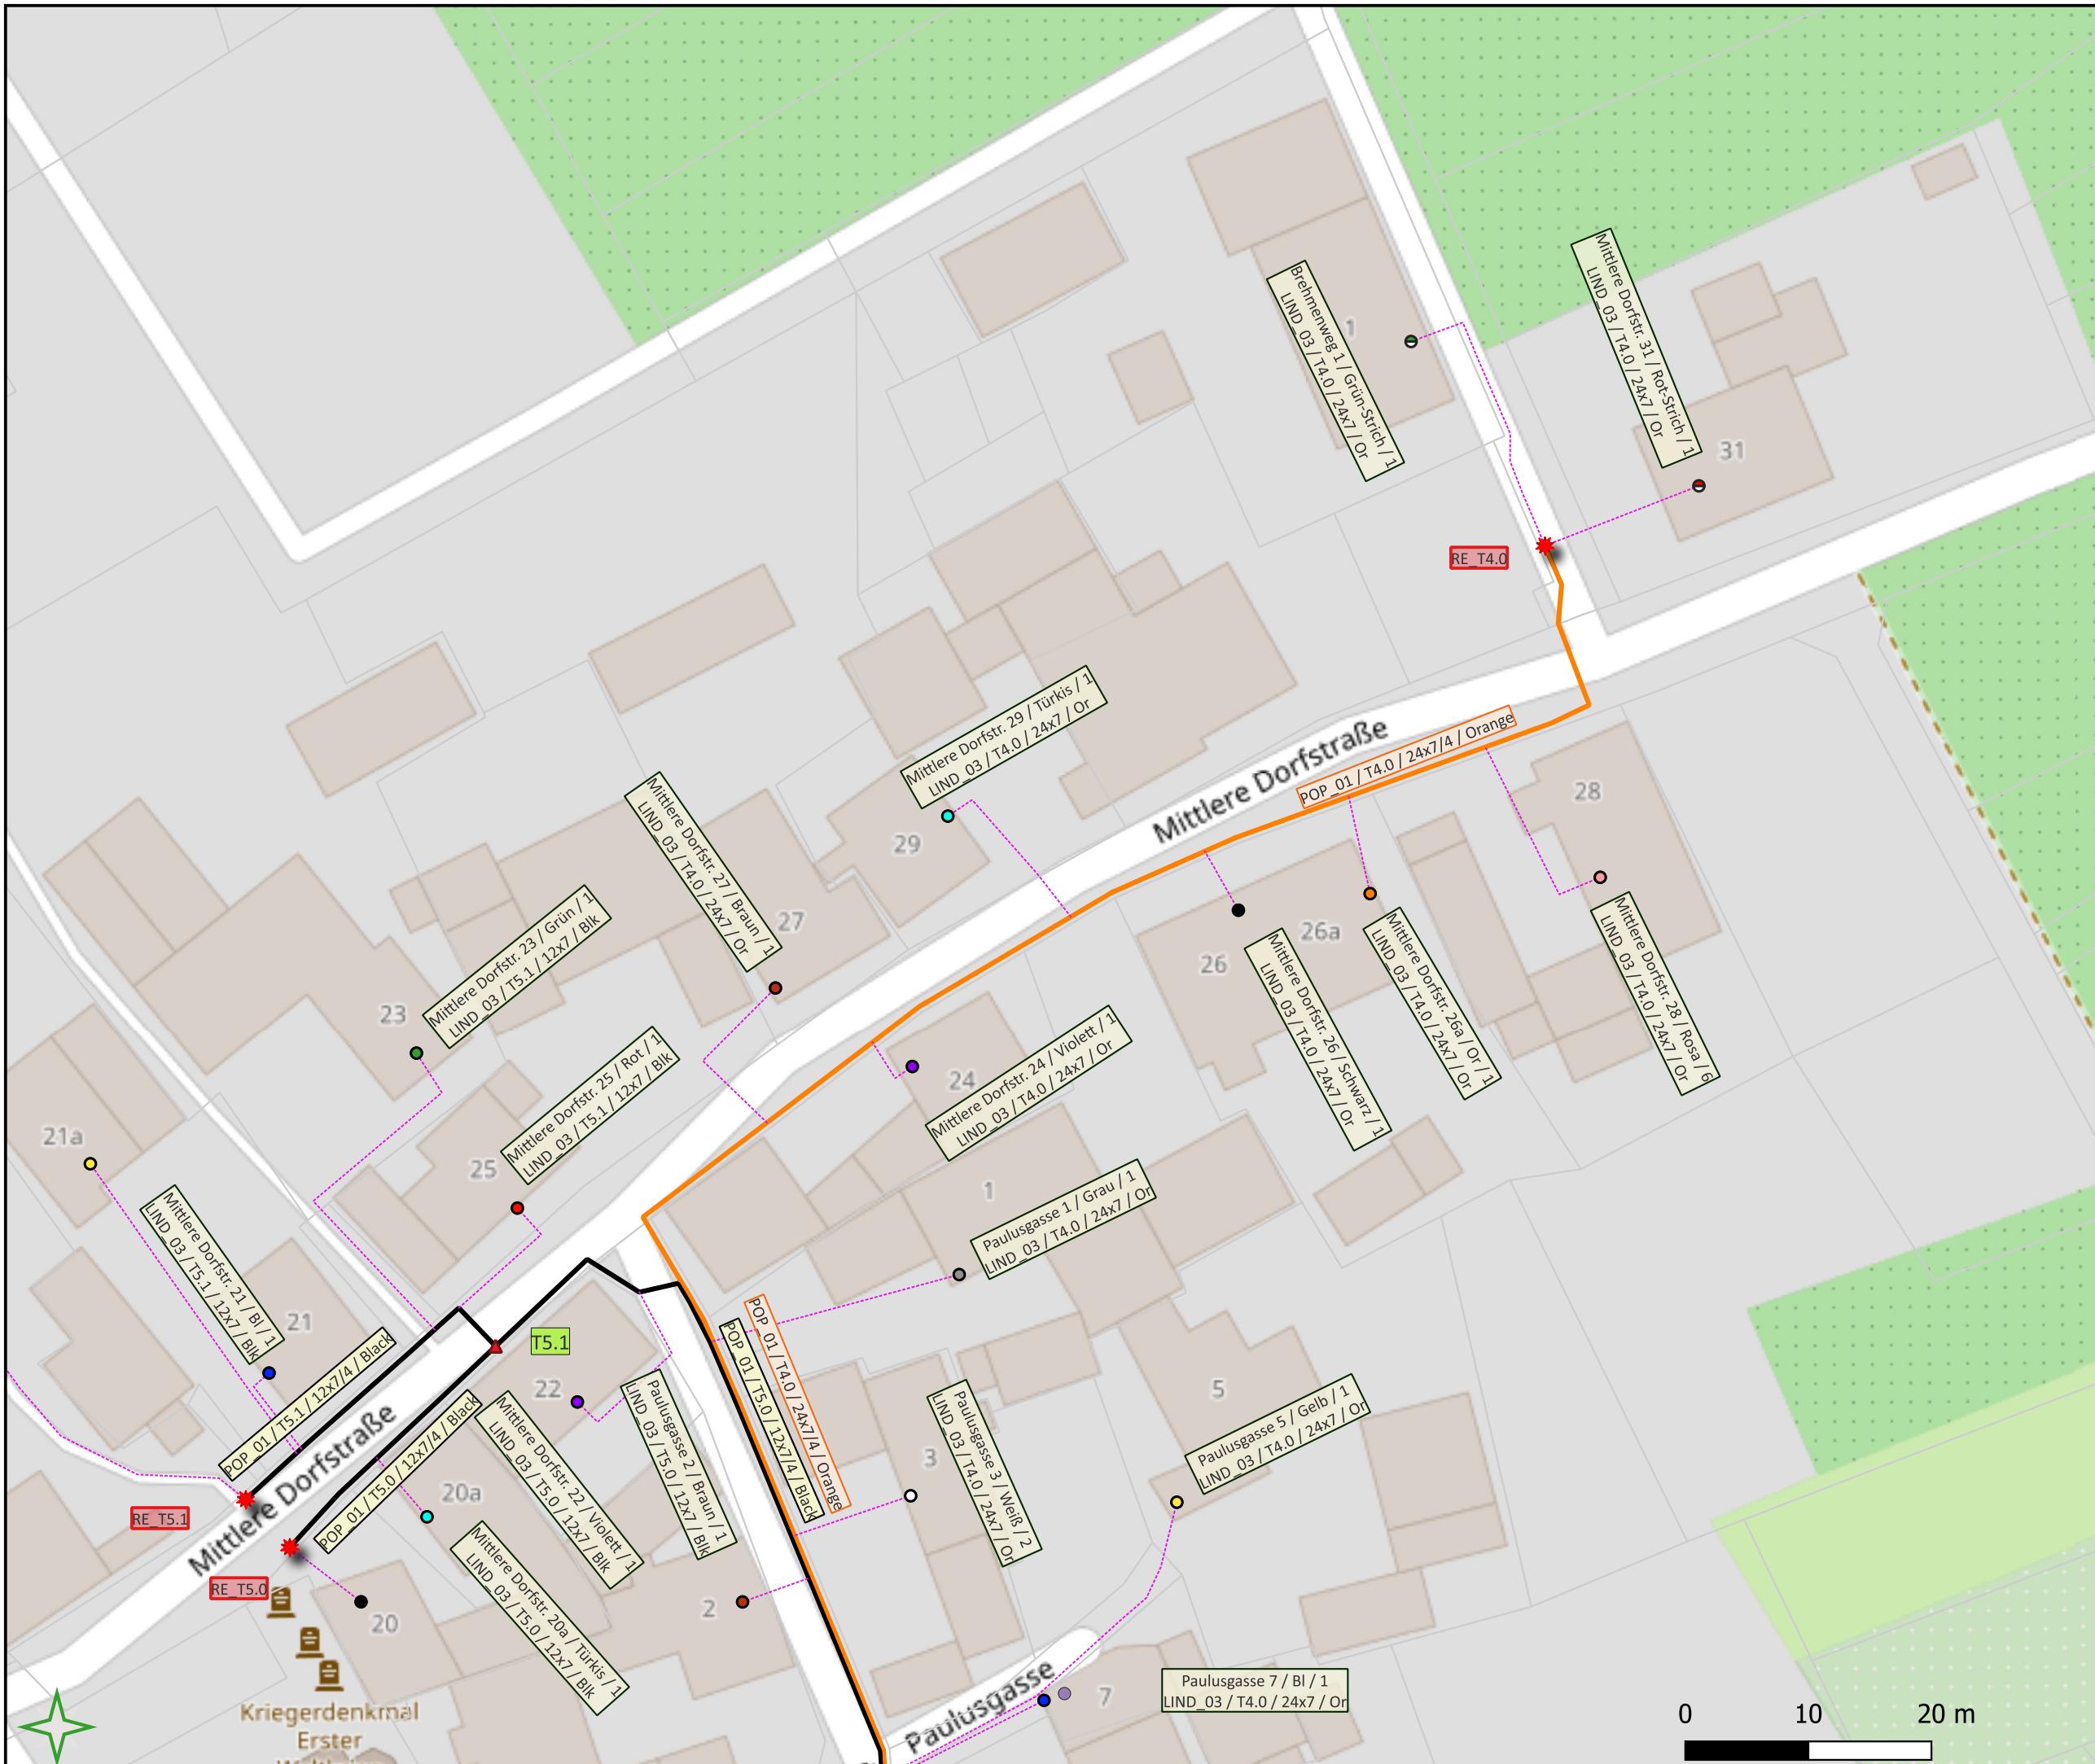

## Punkt

- Adresspoint
  - ★ Duct\_Ende
  - ▲ Duct\_Joint
  - Pop
  - Dp
  - Manhole

## Linee

## ----- Dropduct

## Duct

- Black
  - Blau
  - Green
  - Orange
  - Purple

## Polygon


- Dp\_Cluster
  - POP\_Cluster

DATA

  - Flurstück
  - Backbone

Projekt	Lindelbach
Datum	01.03.2025
Maßstab	1:500
Blatt	LIND_03 20/10
Bearbeiter	Sefa Coskun





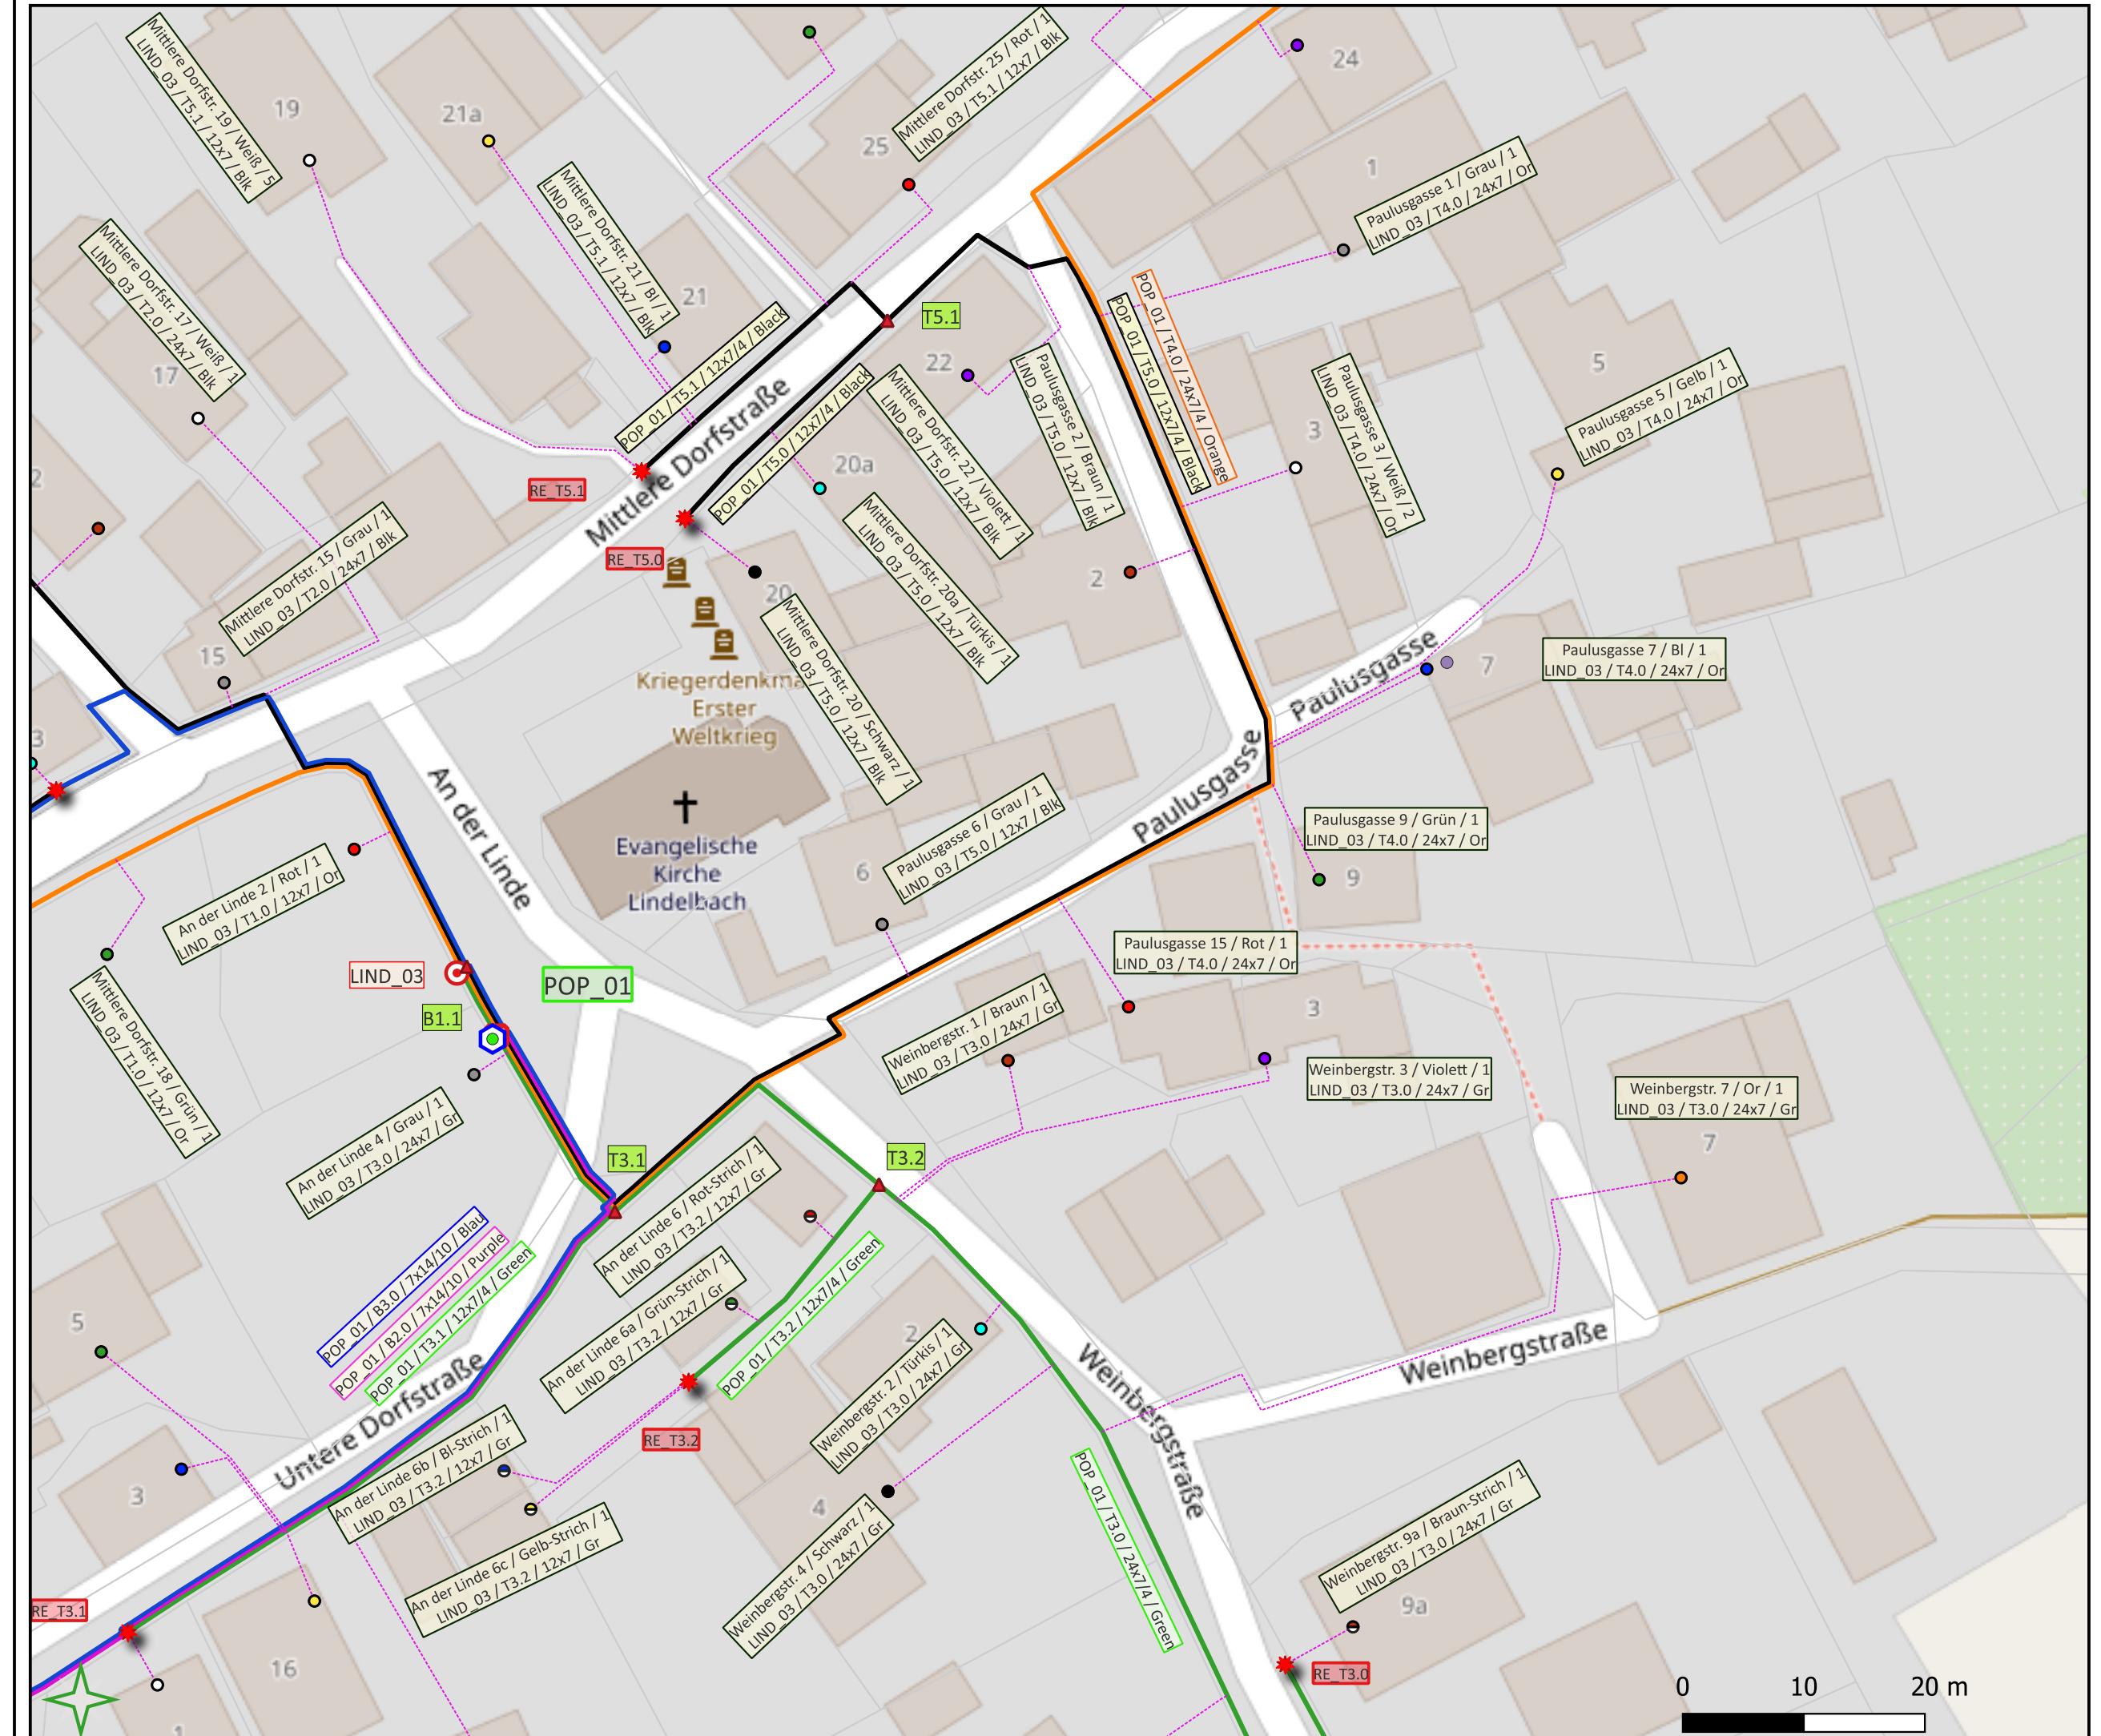

- |            |               |
|------------|---------------|
| Projekt    | Lindelbach    |
| Datum      | 01.03.2025    |
| Maßstab    | 1:500         |
| Blatt      | LIND_03 20/11 |
| Bearbeiter | Sefa Coskun   |

- |            |               |
|------------|---------------|
| Projekt    | Lindelbach    |
| Datum      | 01.03.2025    |
| Maßstab    | 1:500         |
| Blatt      | LIND_03 20/11 |
| Bearbeiter | Sefa Coskun   |



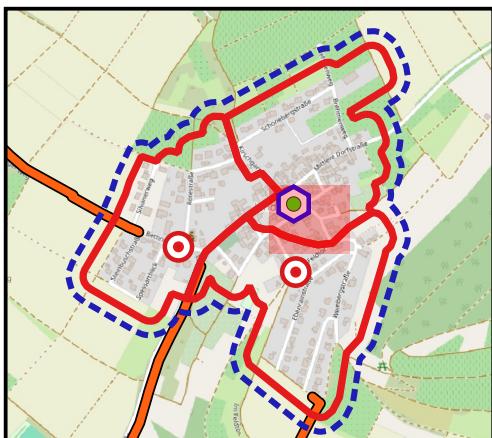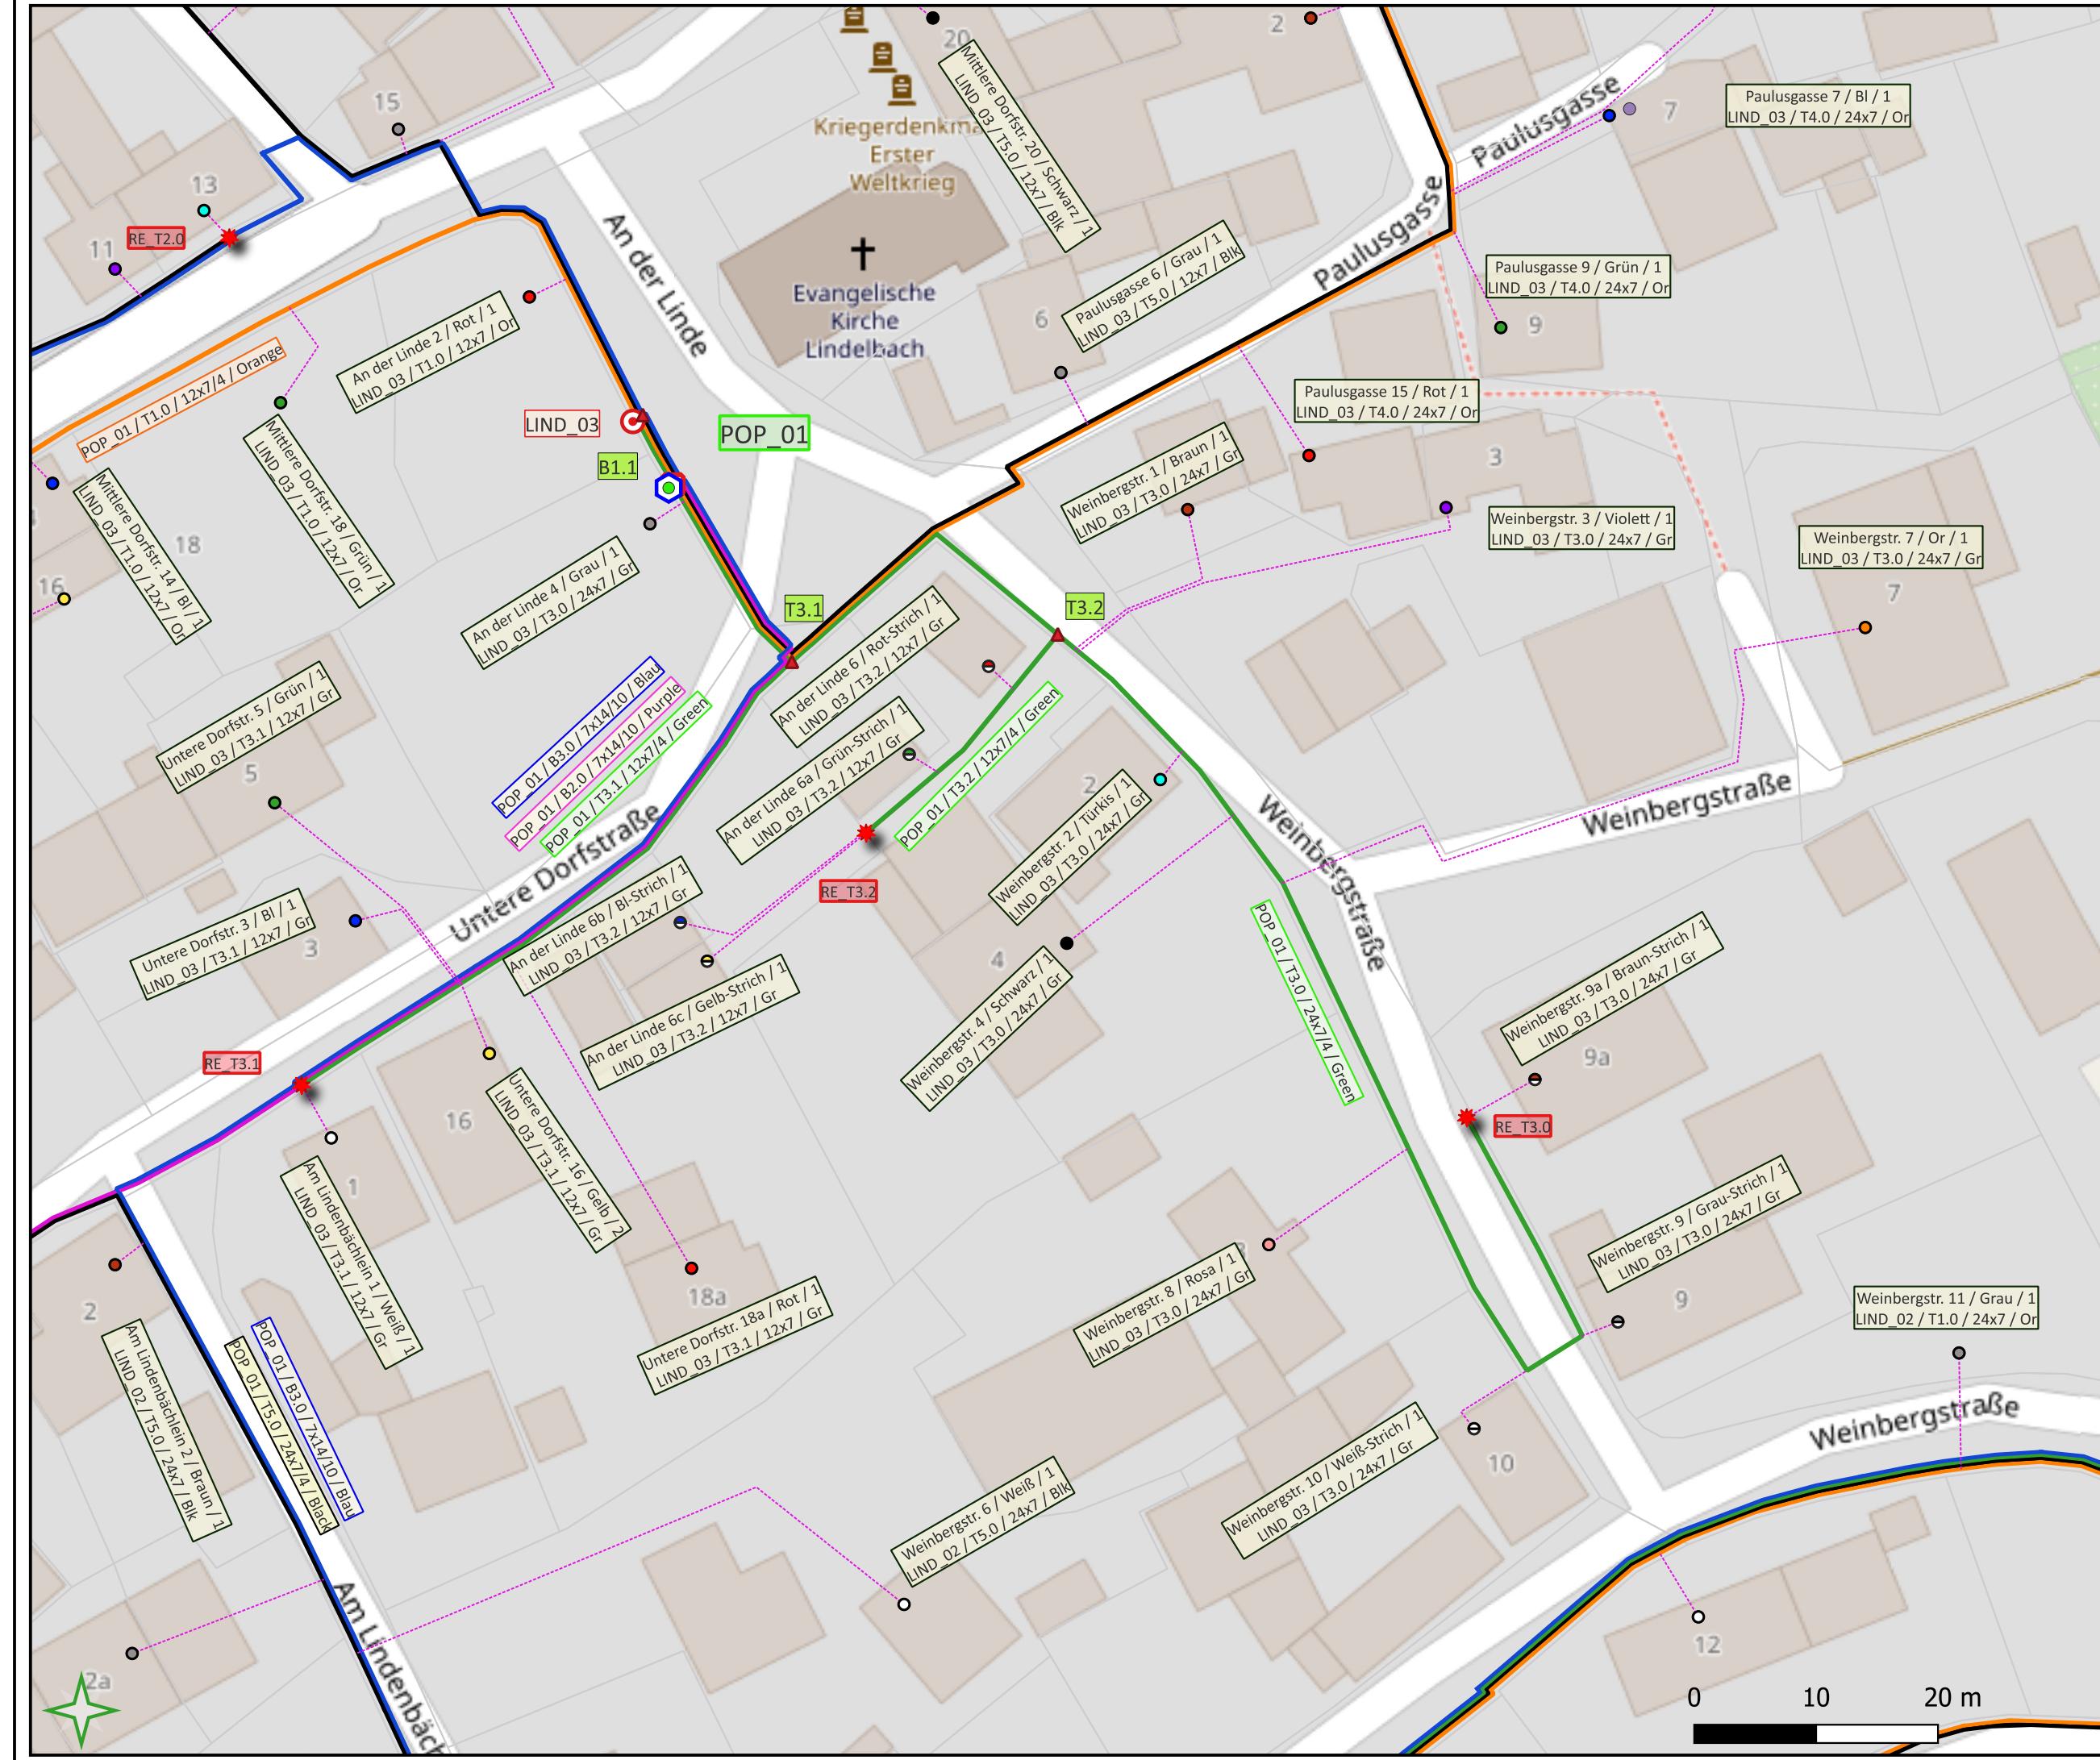

**Punkt**

- Adresspoint
- Duct\_Ende
- Duct\_Joint
- Pop
- Dp
- Manhole

**Linie**

- Dropduct

**Duct**

- Black
- Blau
- Green
- Orange
- Purple



**Polygon**

- Dp\_Cluster
- POP\_Cluster

**DATA**

- Flurstück
- Backbone

Projekt	Lindelbach
Datum	01.03.2025
Maßstab	1:500
Blatt	LIND_03 20/12
Bearbeiter	Sefa Coskun

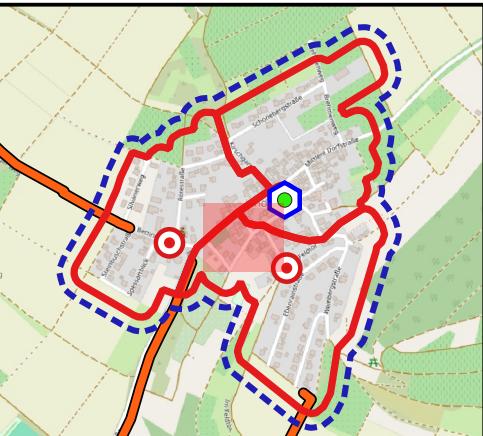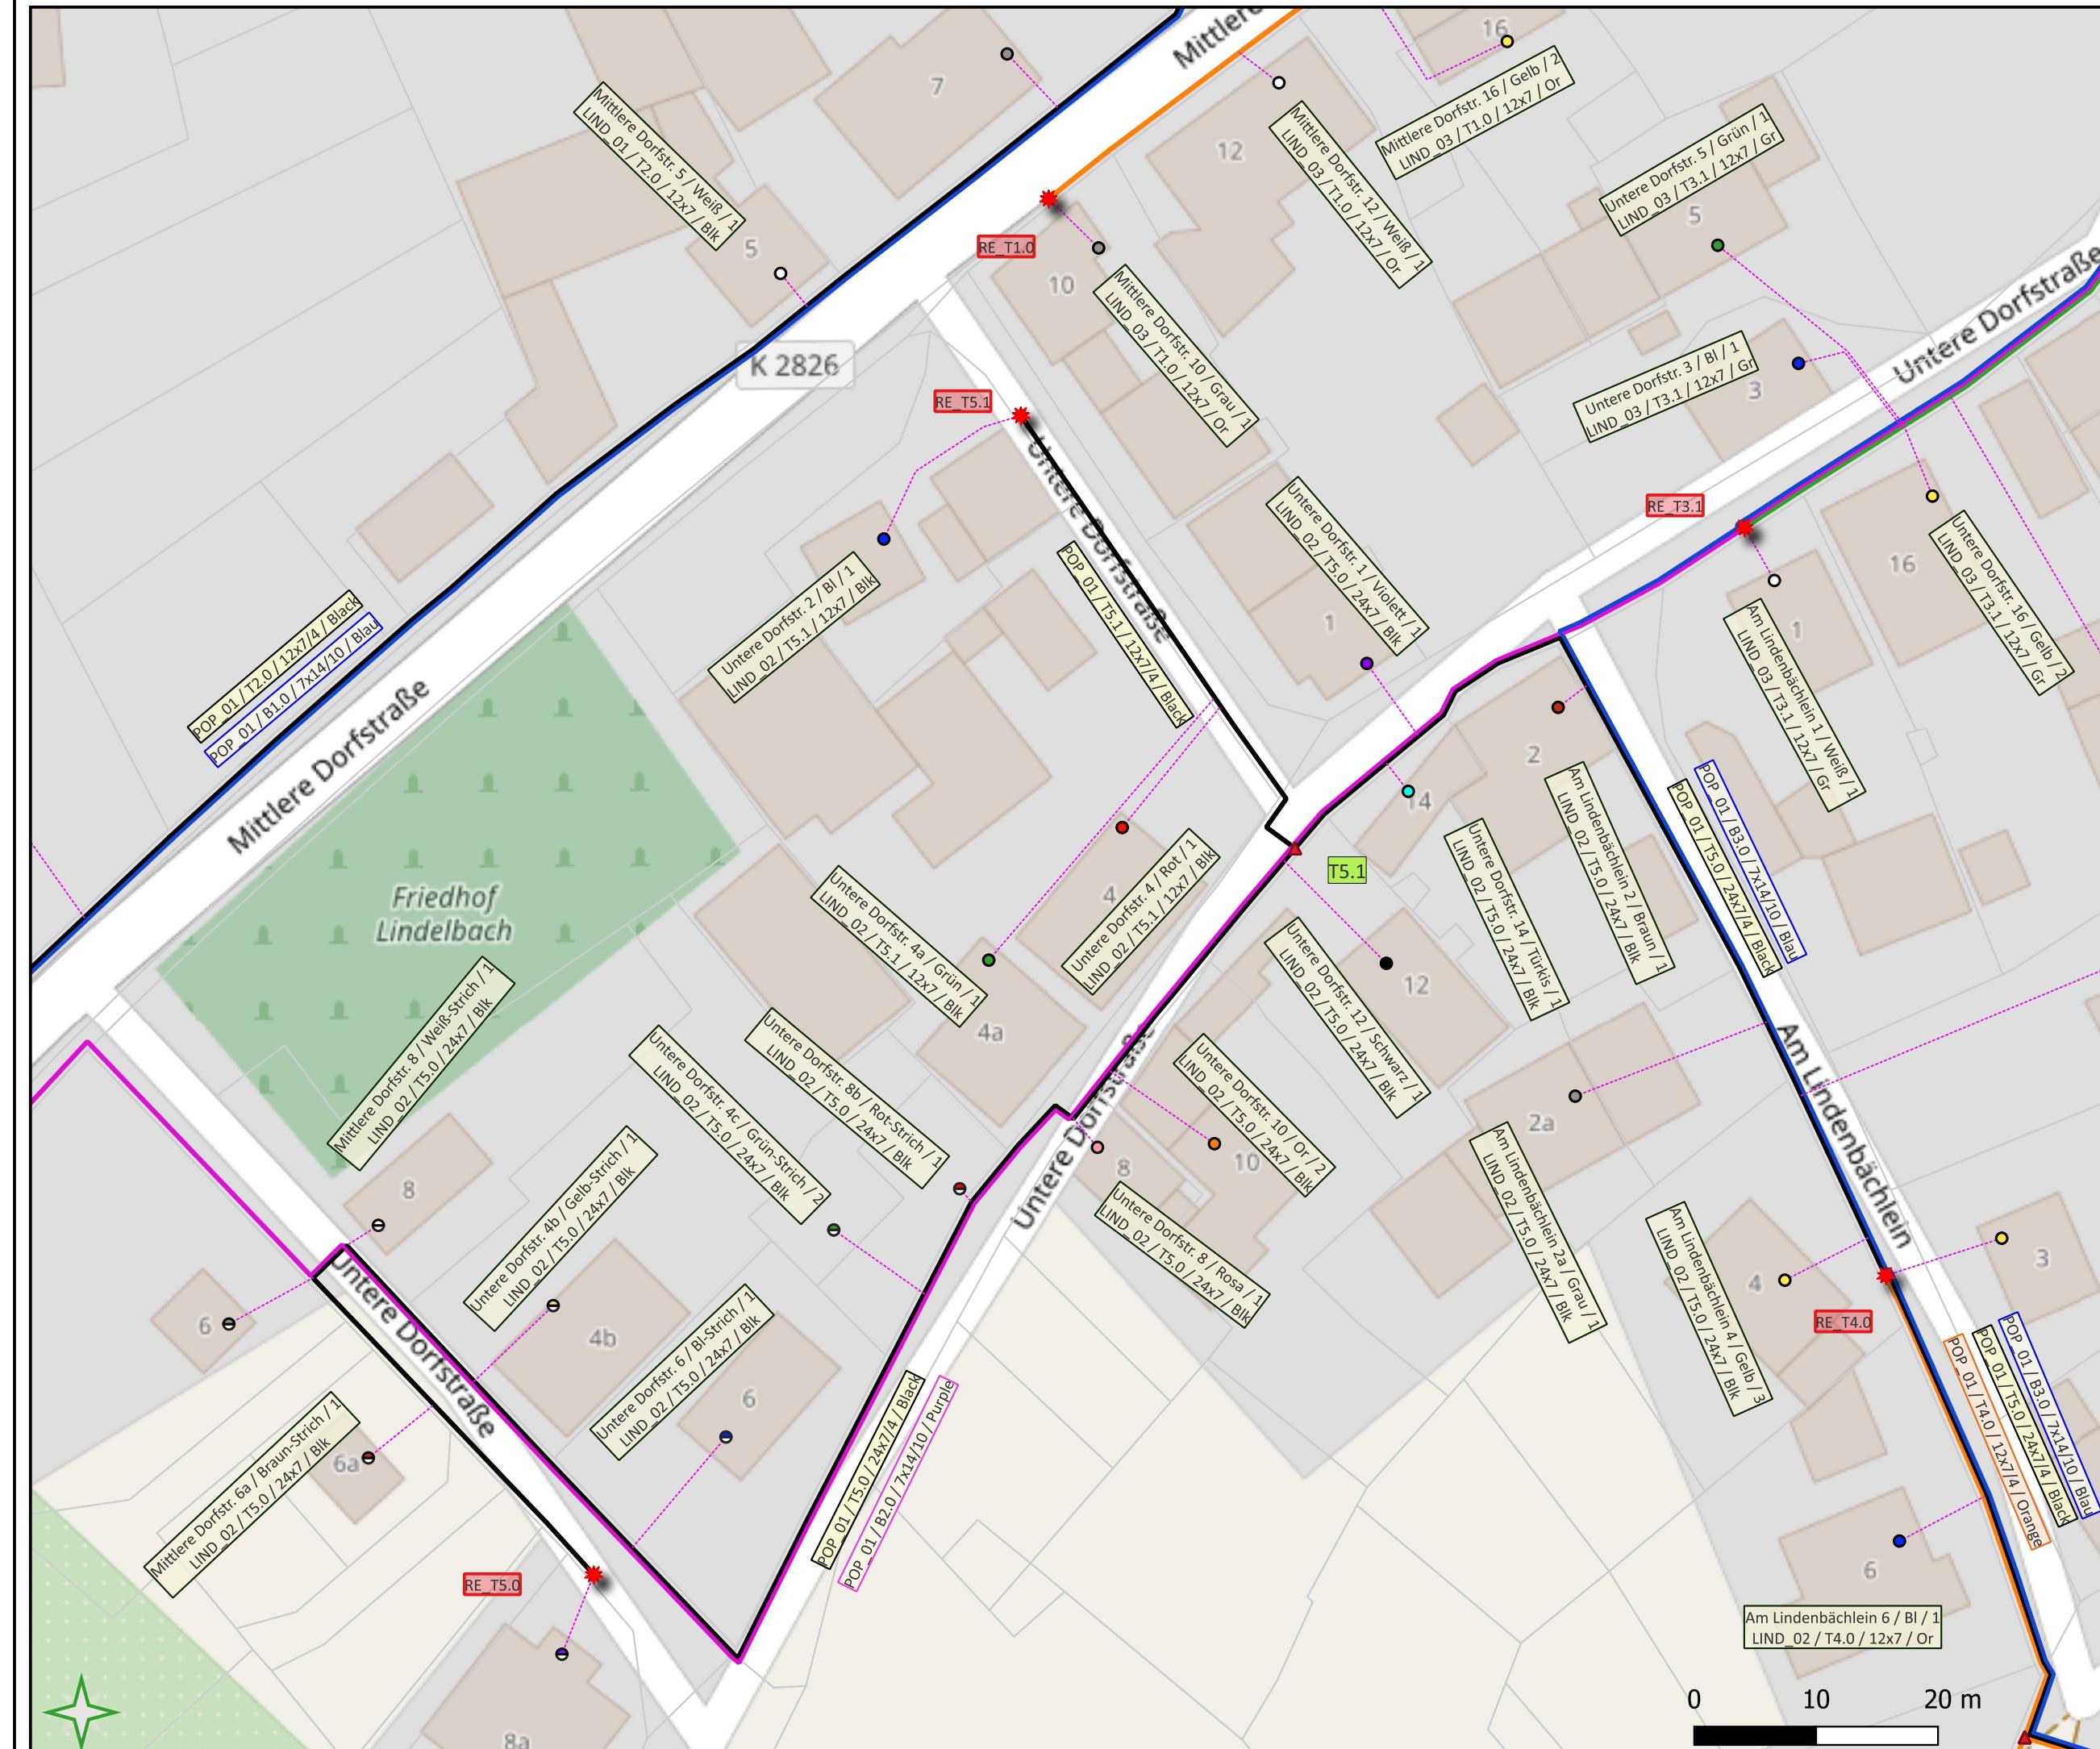

## Punkt

- Adresspoint
  - ★ Duct\_Ende
  - ▲ Duct\_Joint
  - Pop
  - Dp
  - Manhole

### Linie

## Dropduct

## Duct

- Black
  - Blau
  - Green
  - Orange
  - Purple

## Polygon



- Dp\_Cluster  
POP Cluster

DATA

-  Flurstück
  -  Backbone

Projekt	Lindelbach
Datum	01.03.2025
Maßstab	1:500
Blatt	LIND_03 20/13
Bearbeiter	Sefa Coskun



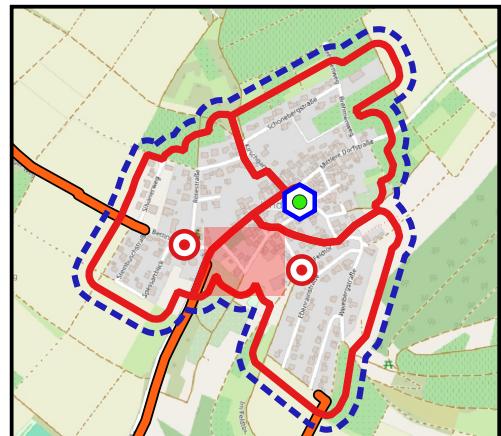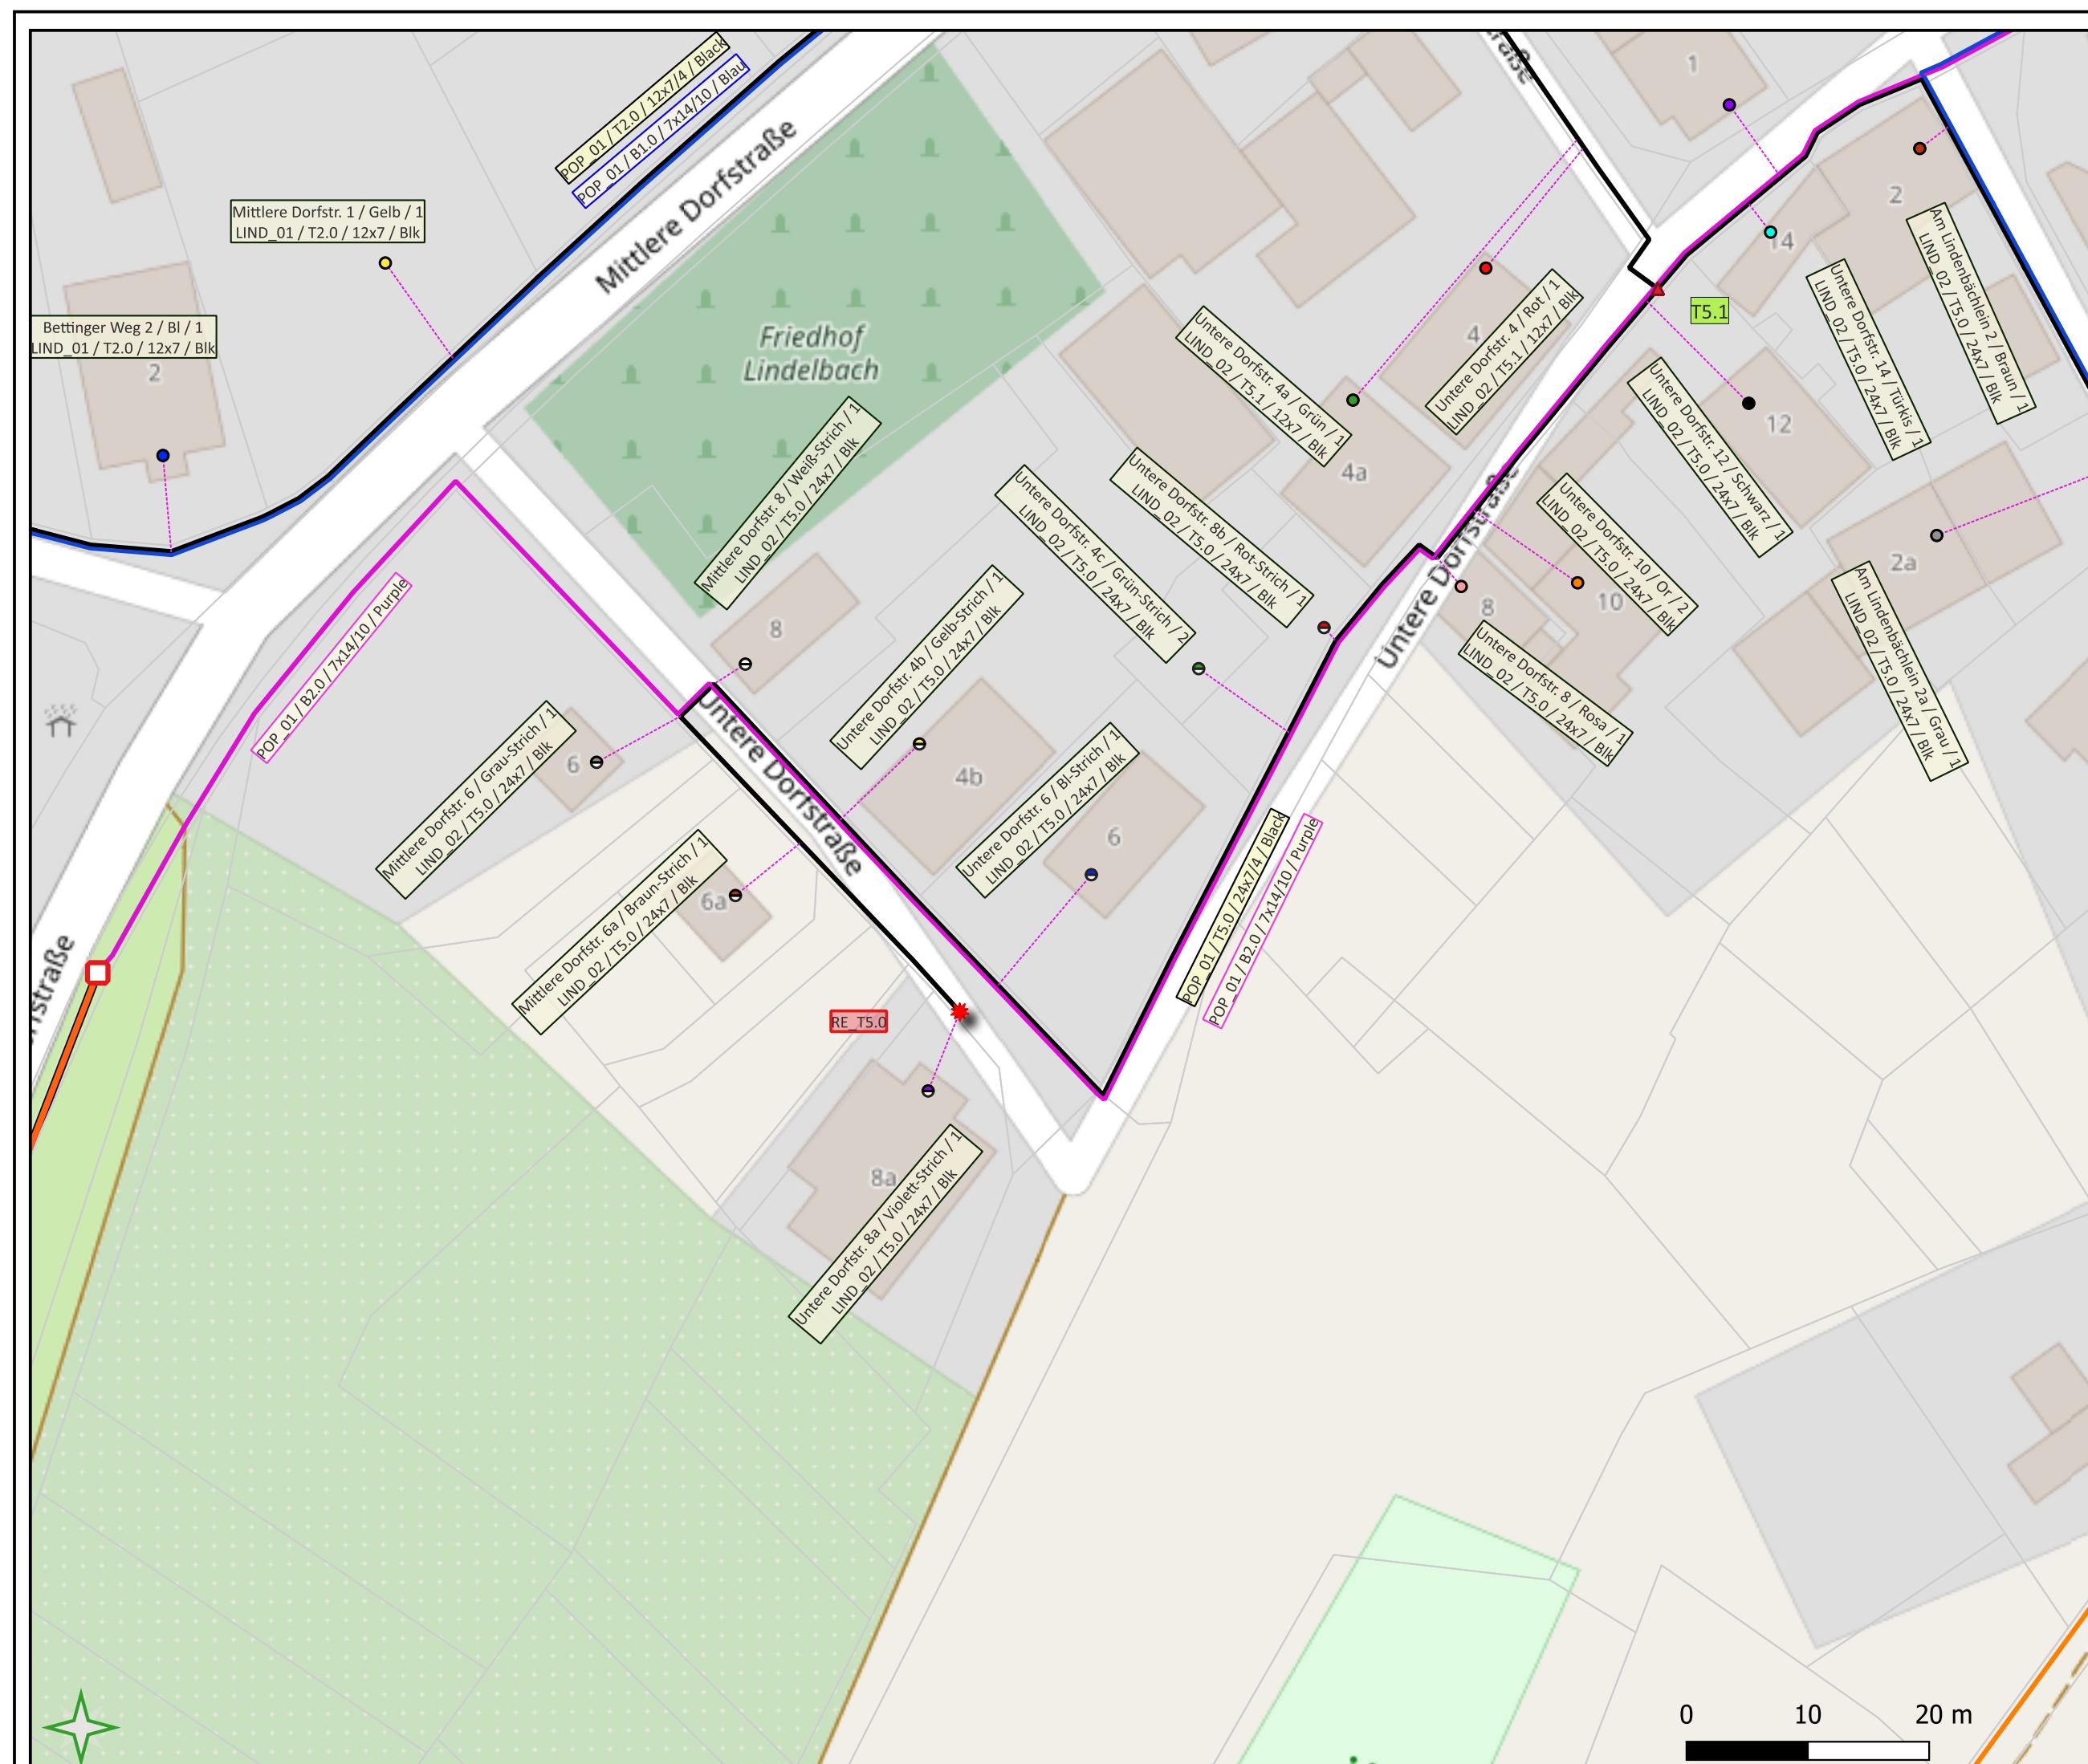

**Punkt**

- Adresspoint
- ★ Duct\_Ende
- ▲ Duct\_Joint
- Pop
- Dp
- Manhole

**Linie**

- - - Dropduct

**Duct**

- Black
- Blue
- Green
- Orange
- Purple



**Polygon**

- Dp\_Cluster
- POP\_Cluster

**DATA**

- Flurstück
- Backbone

Projekt	Lindelbach
Datum	01.03.2025
Maßstab	1:500
Blatt	LIND_02 20/14
Bearbeiter	Sefa Coskun

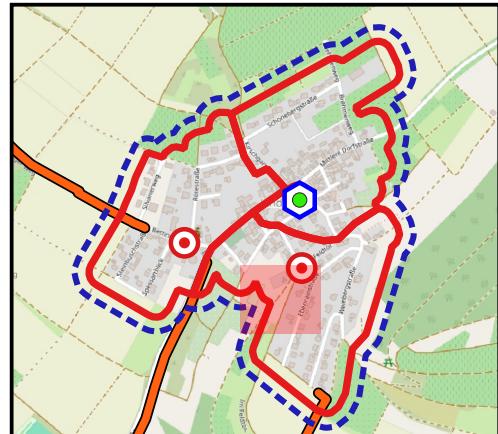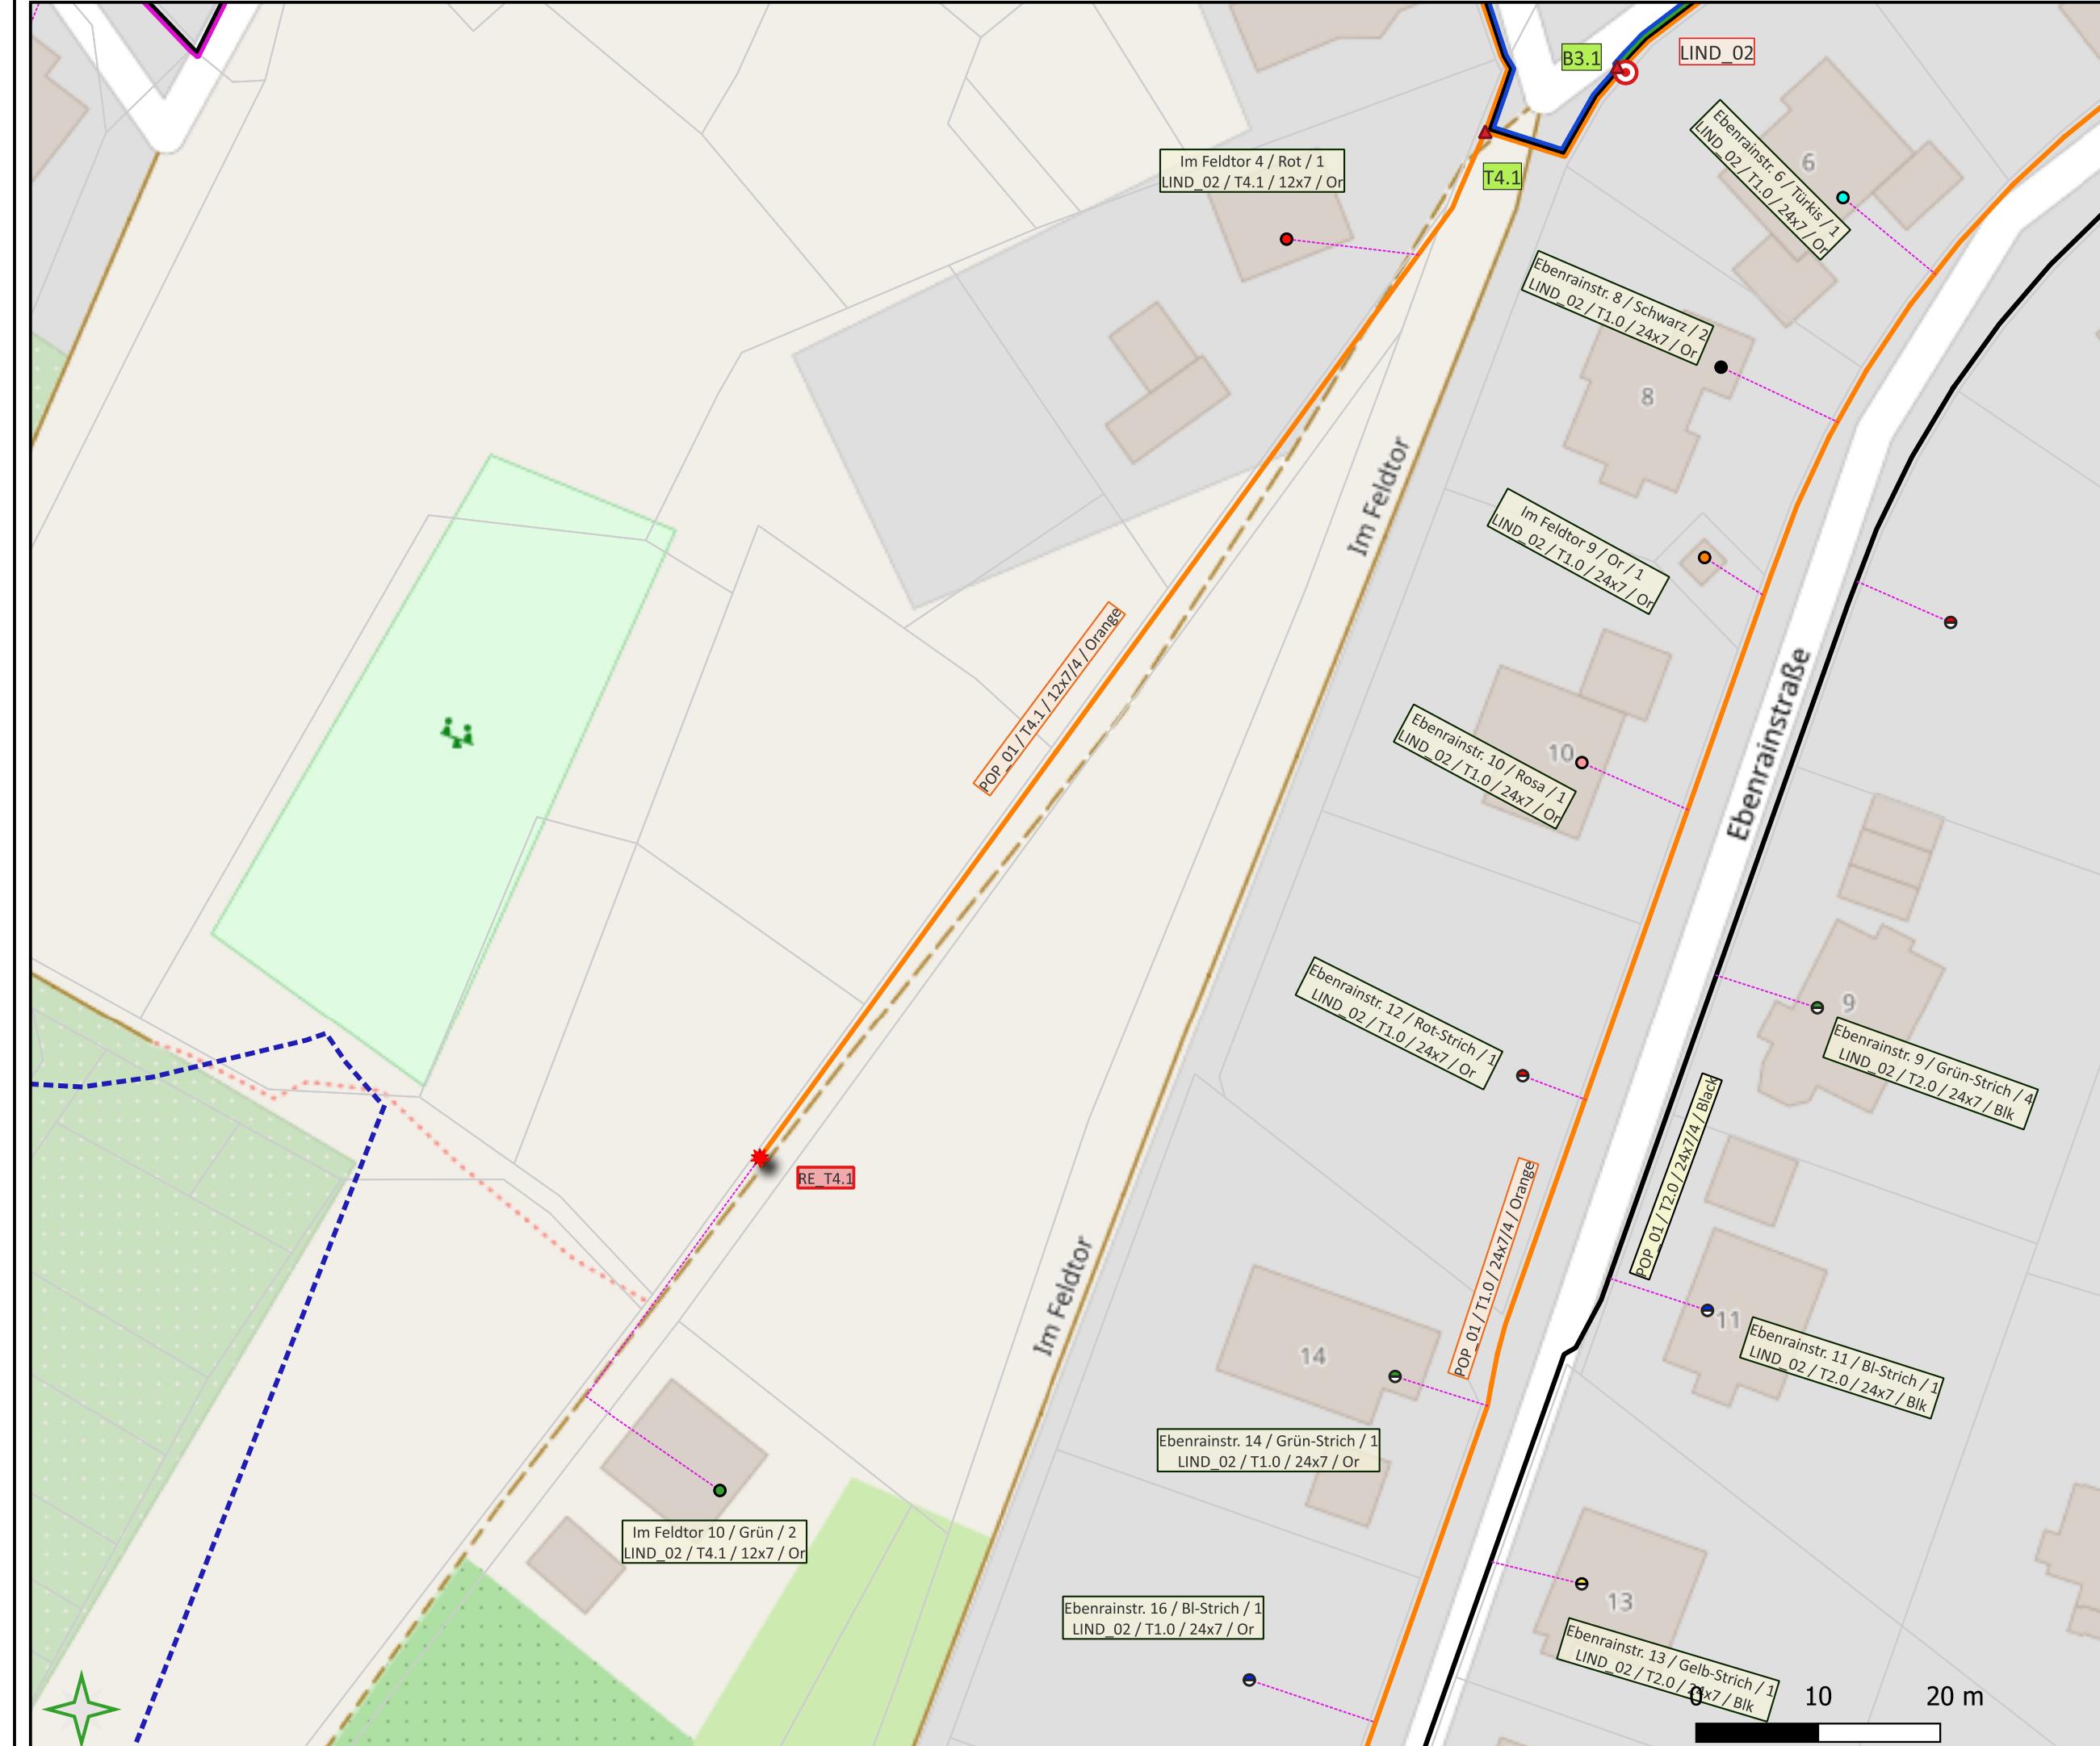

#### Punkt

- Adresspoint
- \* Duct\_Ende
- ▲ Duct\_Joint
- Pop
- Dp
- Manhole

#### Linie

- Dropduct

#### Duct

- Black
- Blue
- Green
- Orange
- Purple


#### Polygon

- Dp\_Cluster
- POP\_Cluster

#### DATA

- Flurstück
- Backbone

Projekt	Lindelbach
Datum	01.03.2025
Maßstab	1:500
Blatt	LIND_02 20/15
Bearbeiter	Sefa Coskun

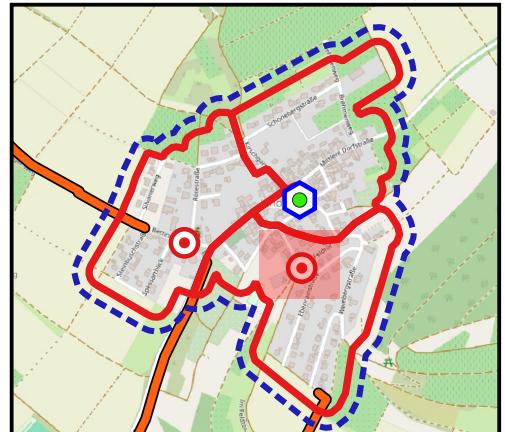

**Punkt**

- Adresspoint
- \* Duct\_Ende
- ▲ Duct\_Joint
- Pop
- Dp
- Manhole

**Linie**

- Dropduct

**Duct**

- Black
- Blau
- Green
- Orange
- Purple


**Polygon**

- Dp\_Cluster
- POP\_Cluster



**DATA**

- Flurstück
- Backbone

Projekt | Lindelbach  
 Datum | 01.03.2025  
 Maßstab | 1:500  
 Blatt | LIND\_02 20/16  
 Bearbeiter | Sefa Coskun

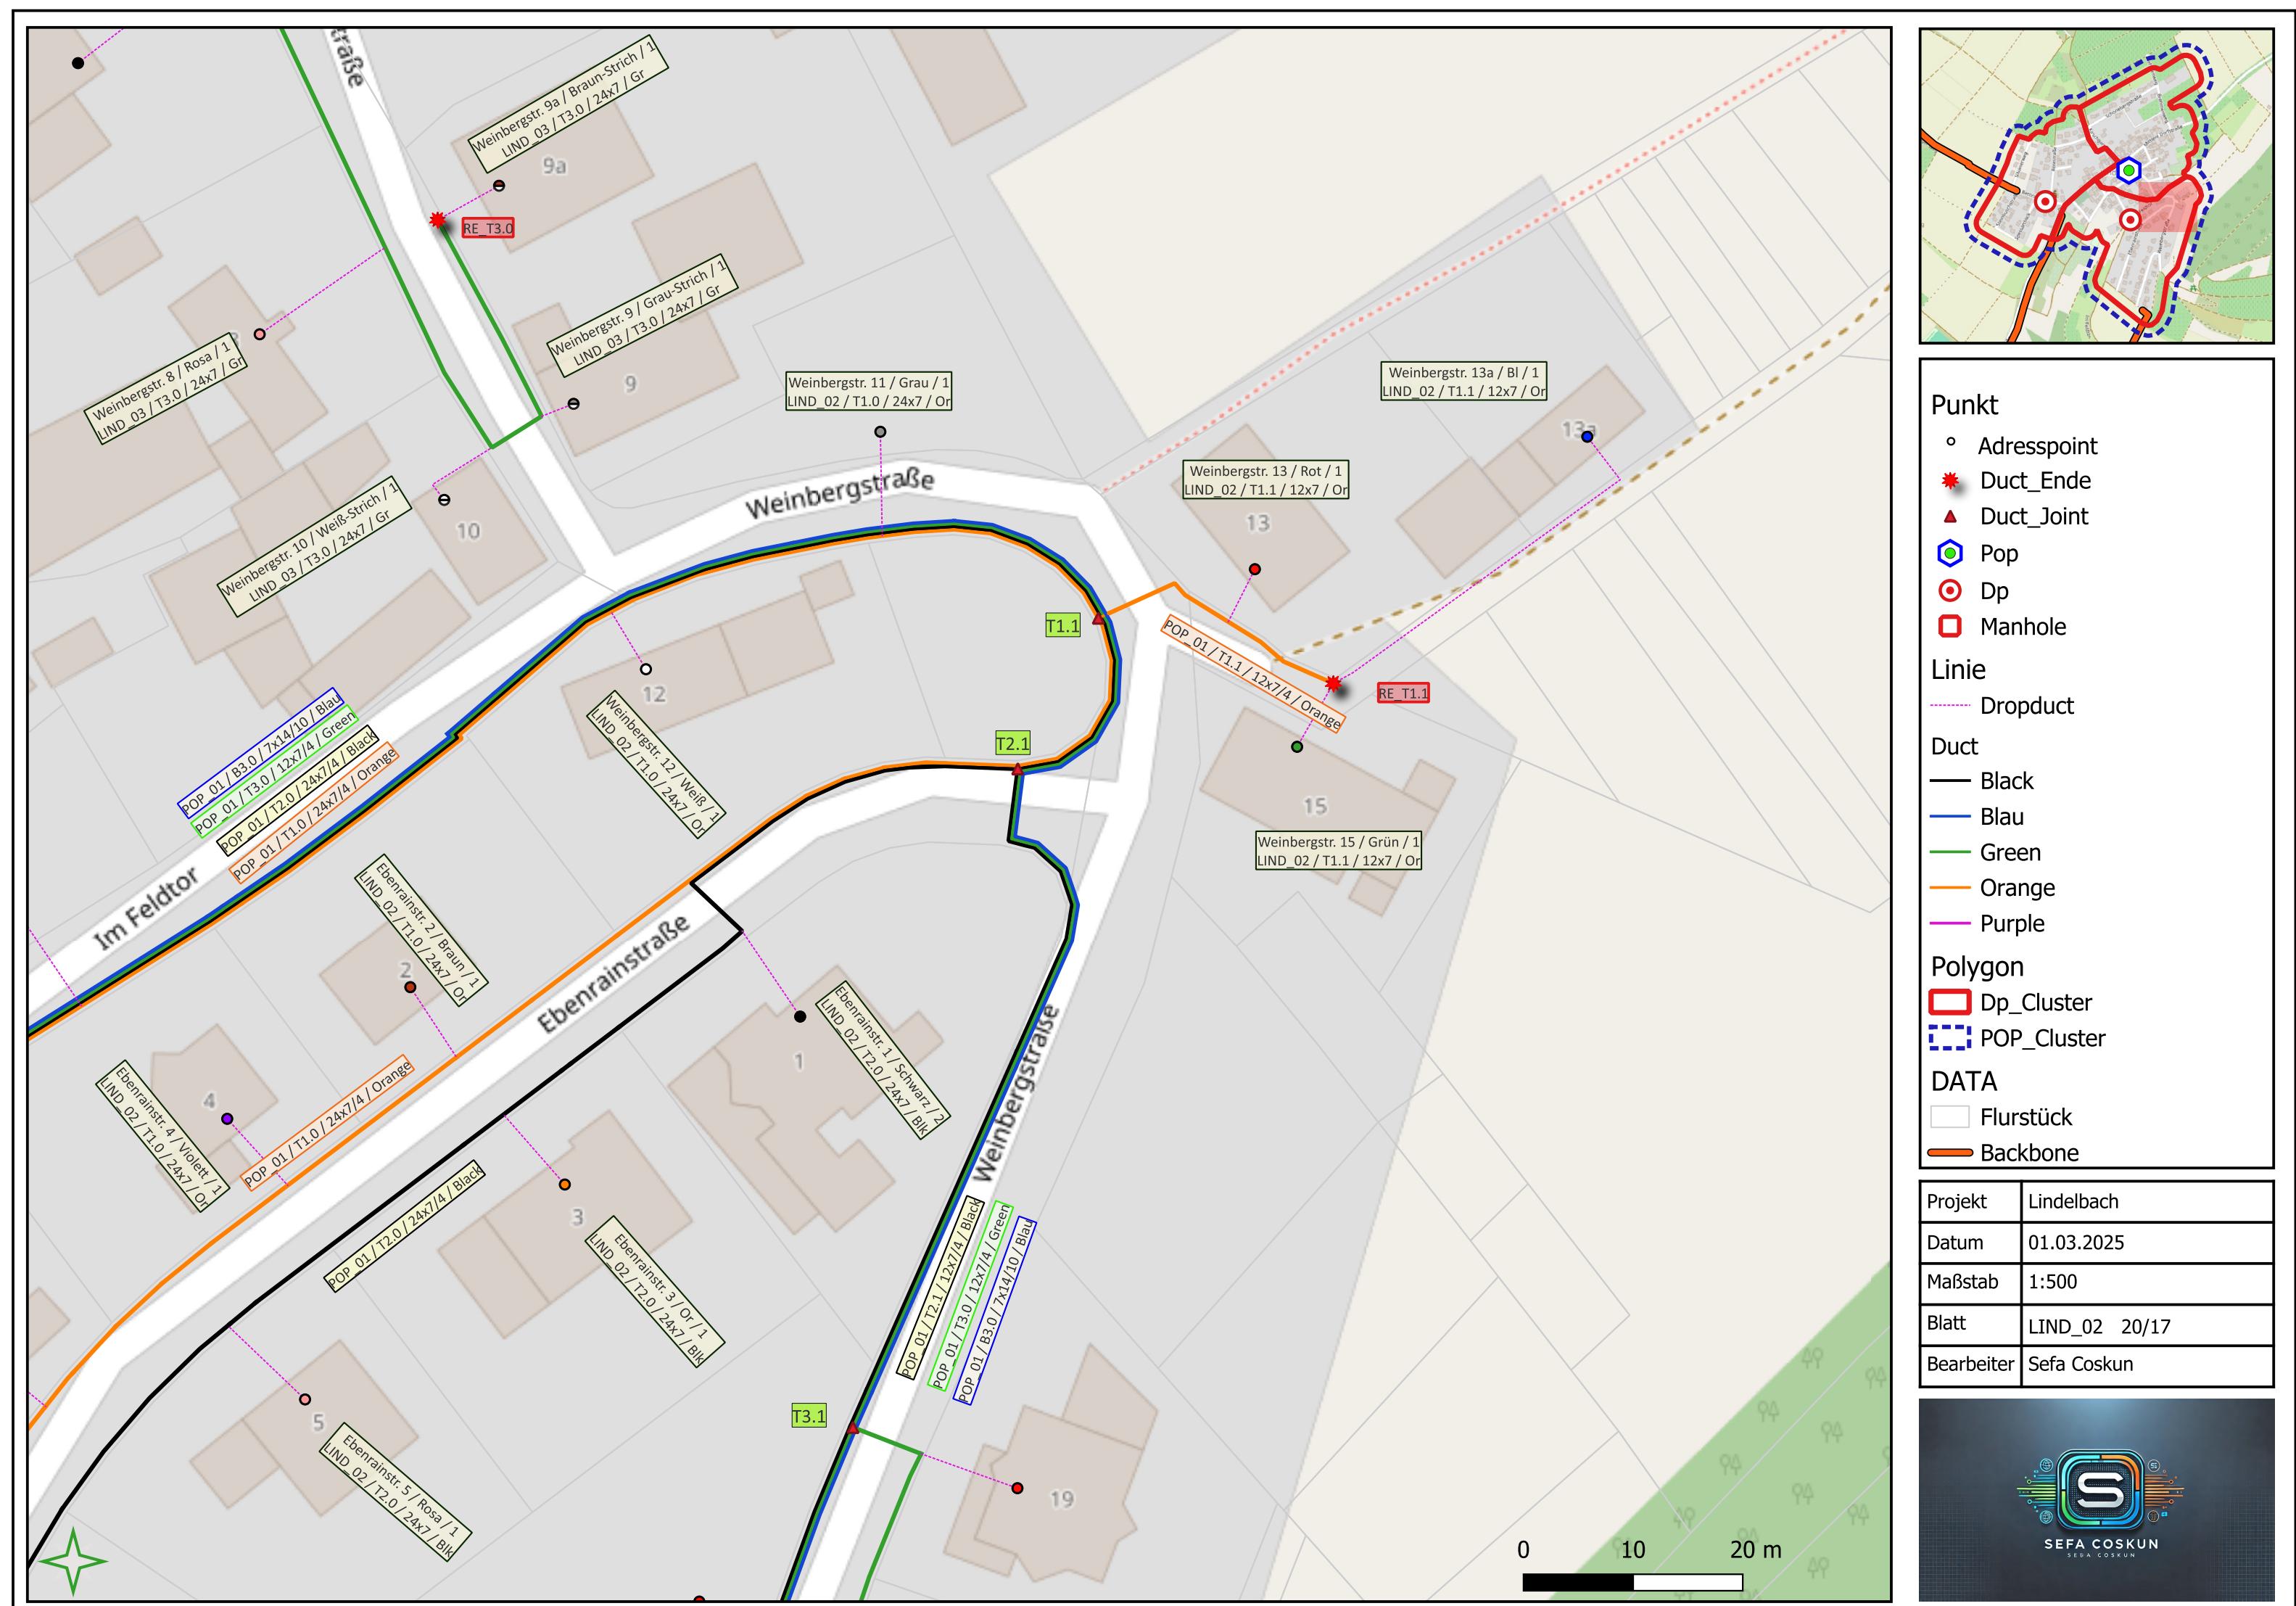



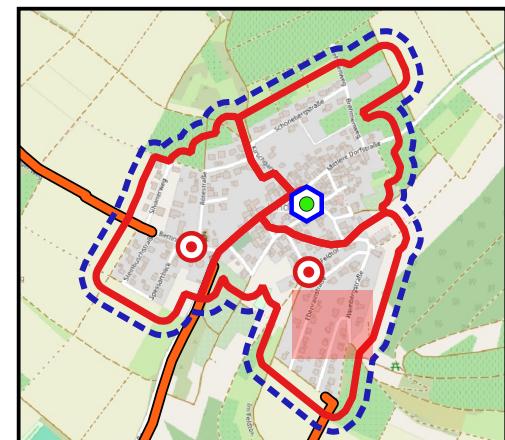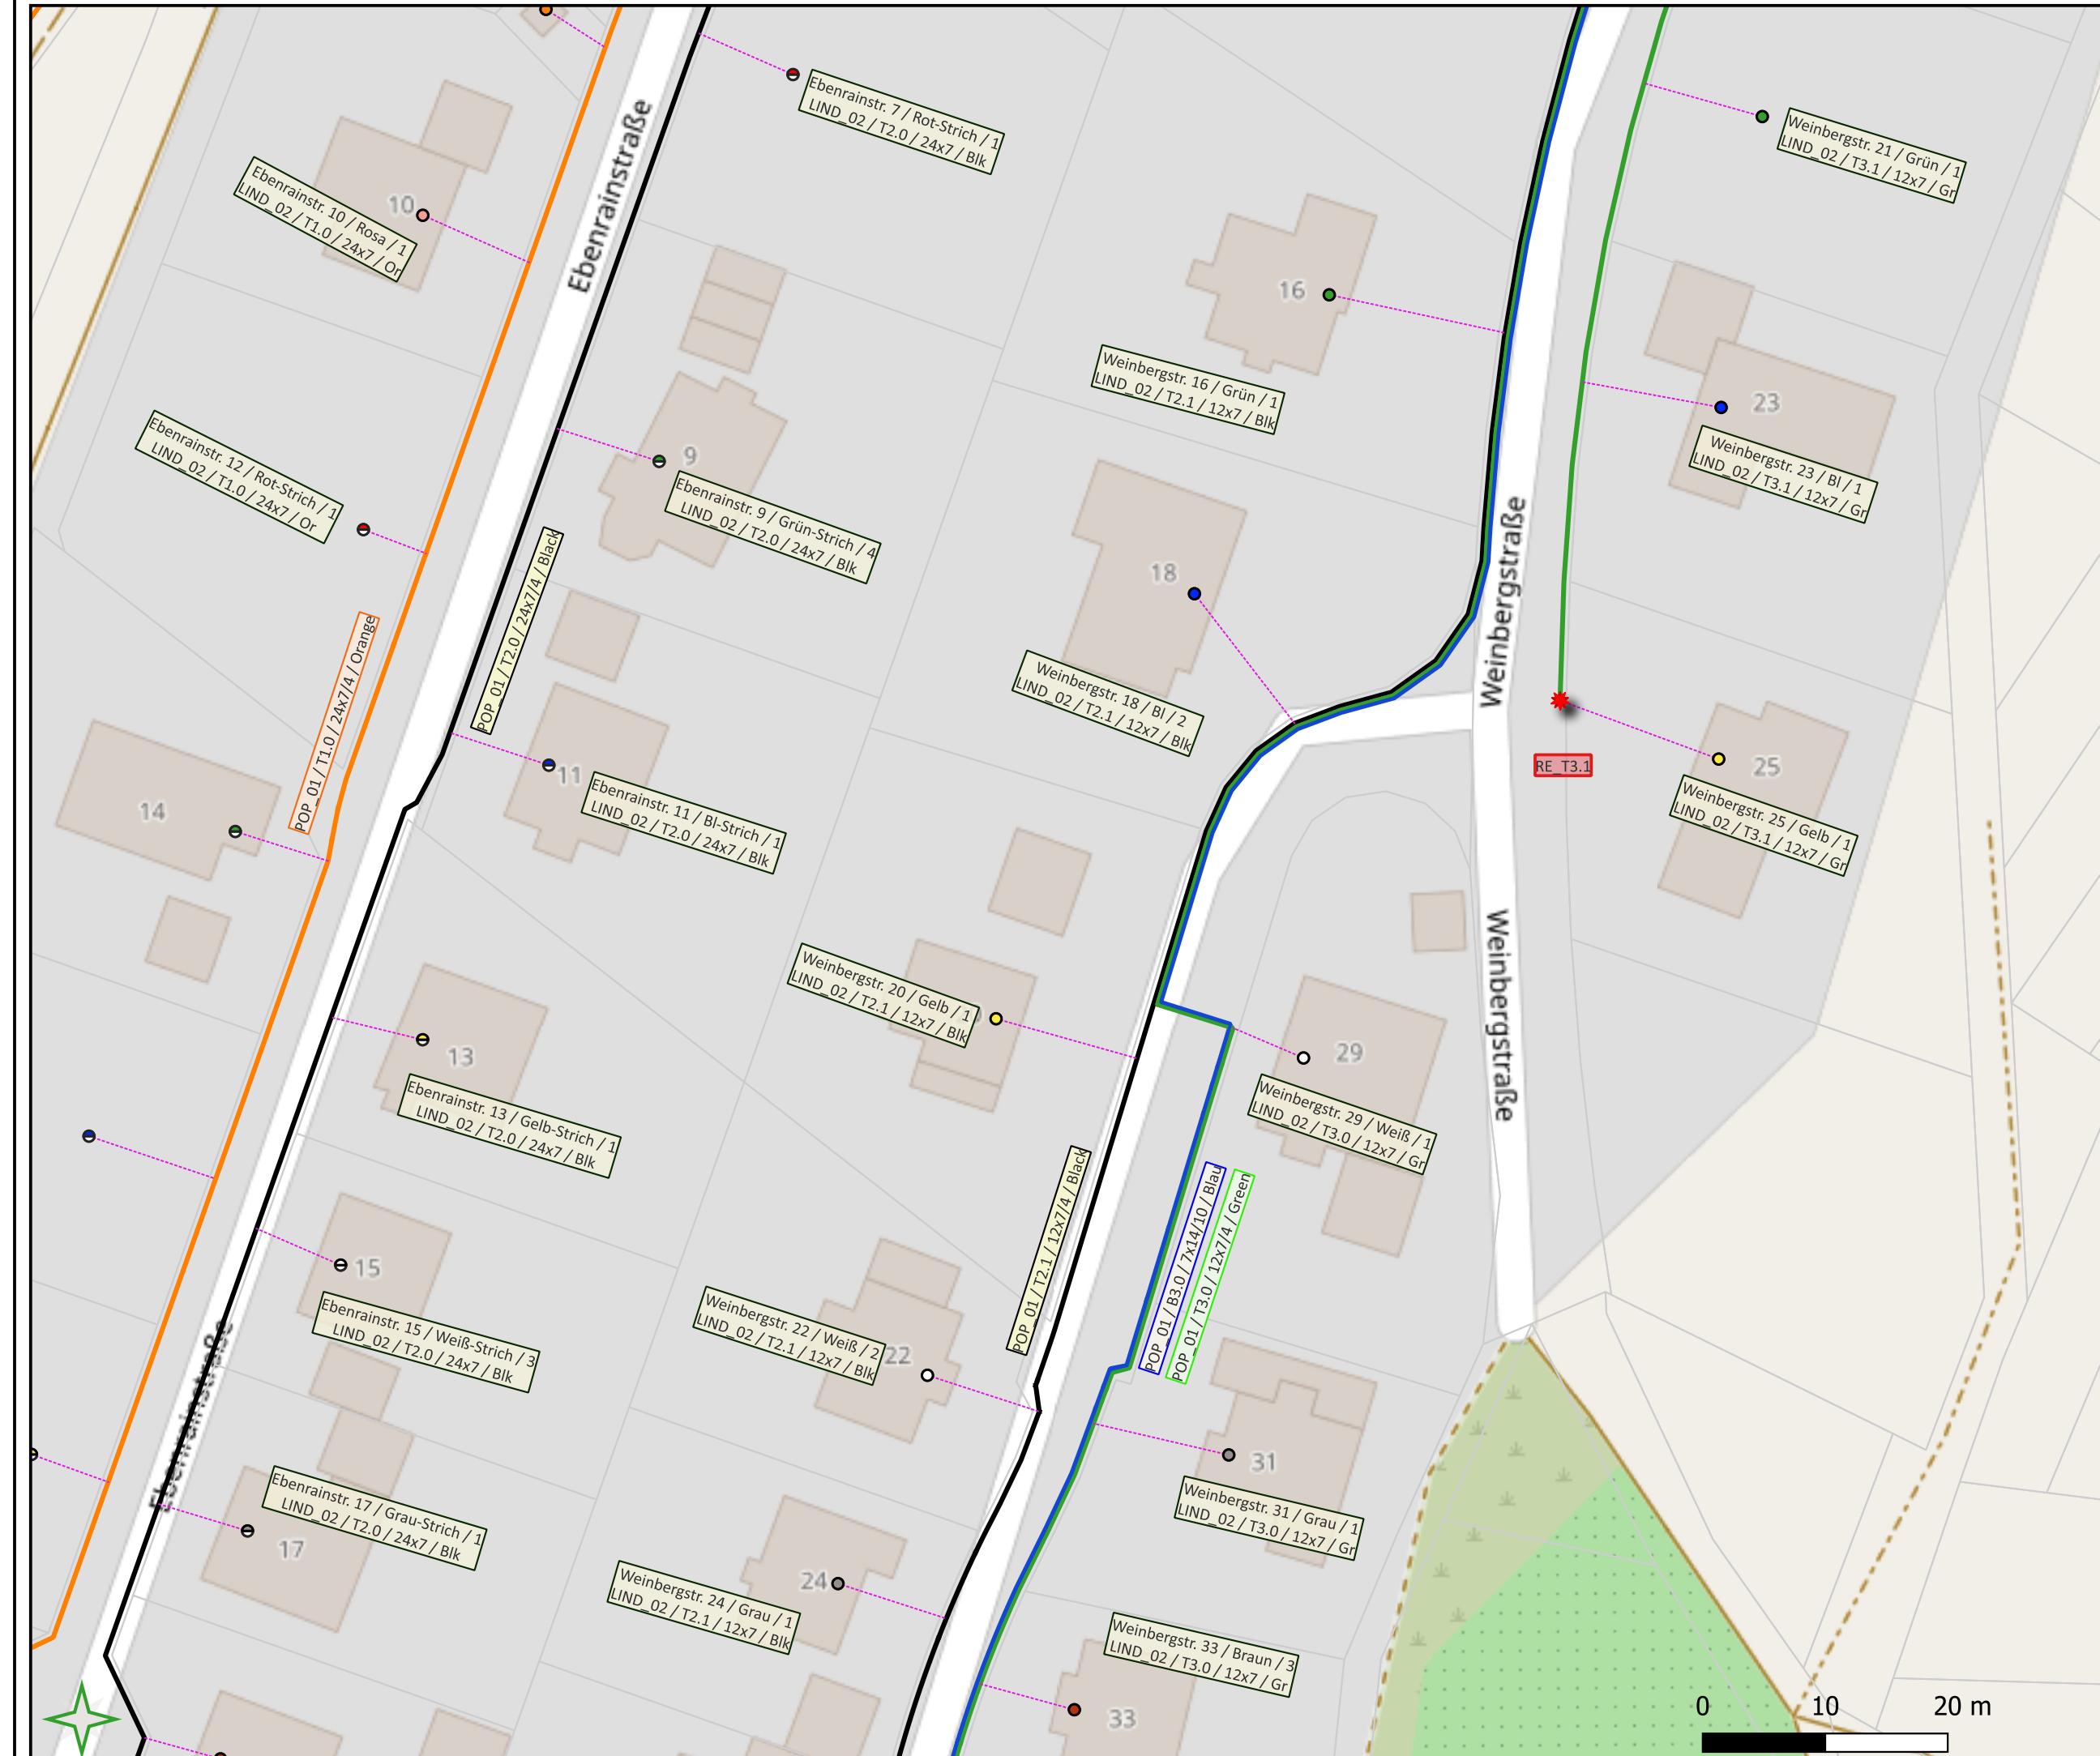

#### Punkt

- Adresspoint
- \* Duct\_Ende
- ▲ Duct\_Joint
- Pop
- Dp
- Manhole

#### Linie

- Dropduct

#### Duct

- Black
- Blue
- Green
- Orange
- Purple

#### Polygon

- Dp\_Cluster
- POP\_Cluster

#### DATA

- Flurstück
- Backbone

Projekt	Lindelbach
Datum	01.03.2025
Maßstab	1:500
Blatt	LIND_02 20/19
Bearbeiter	Sefa Coskun



